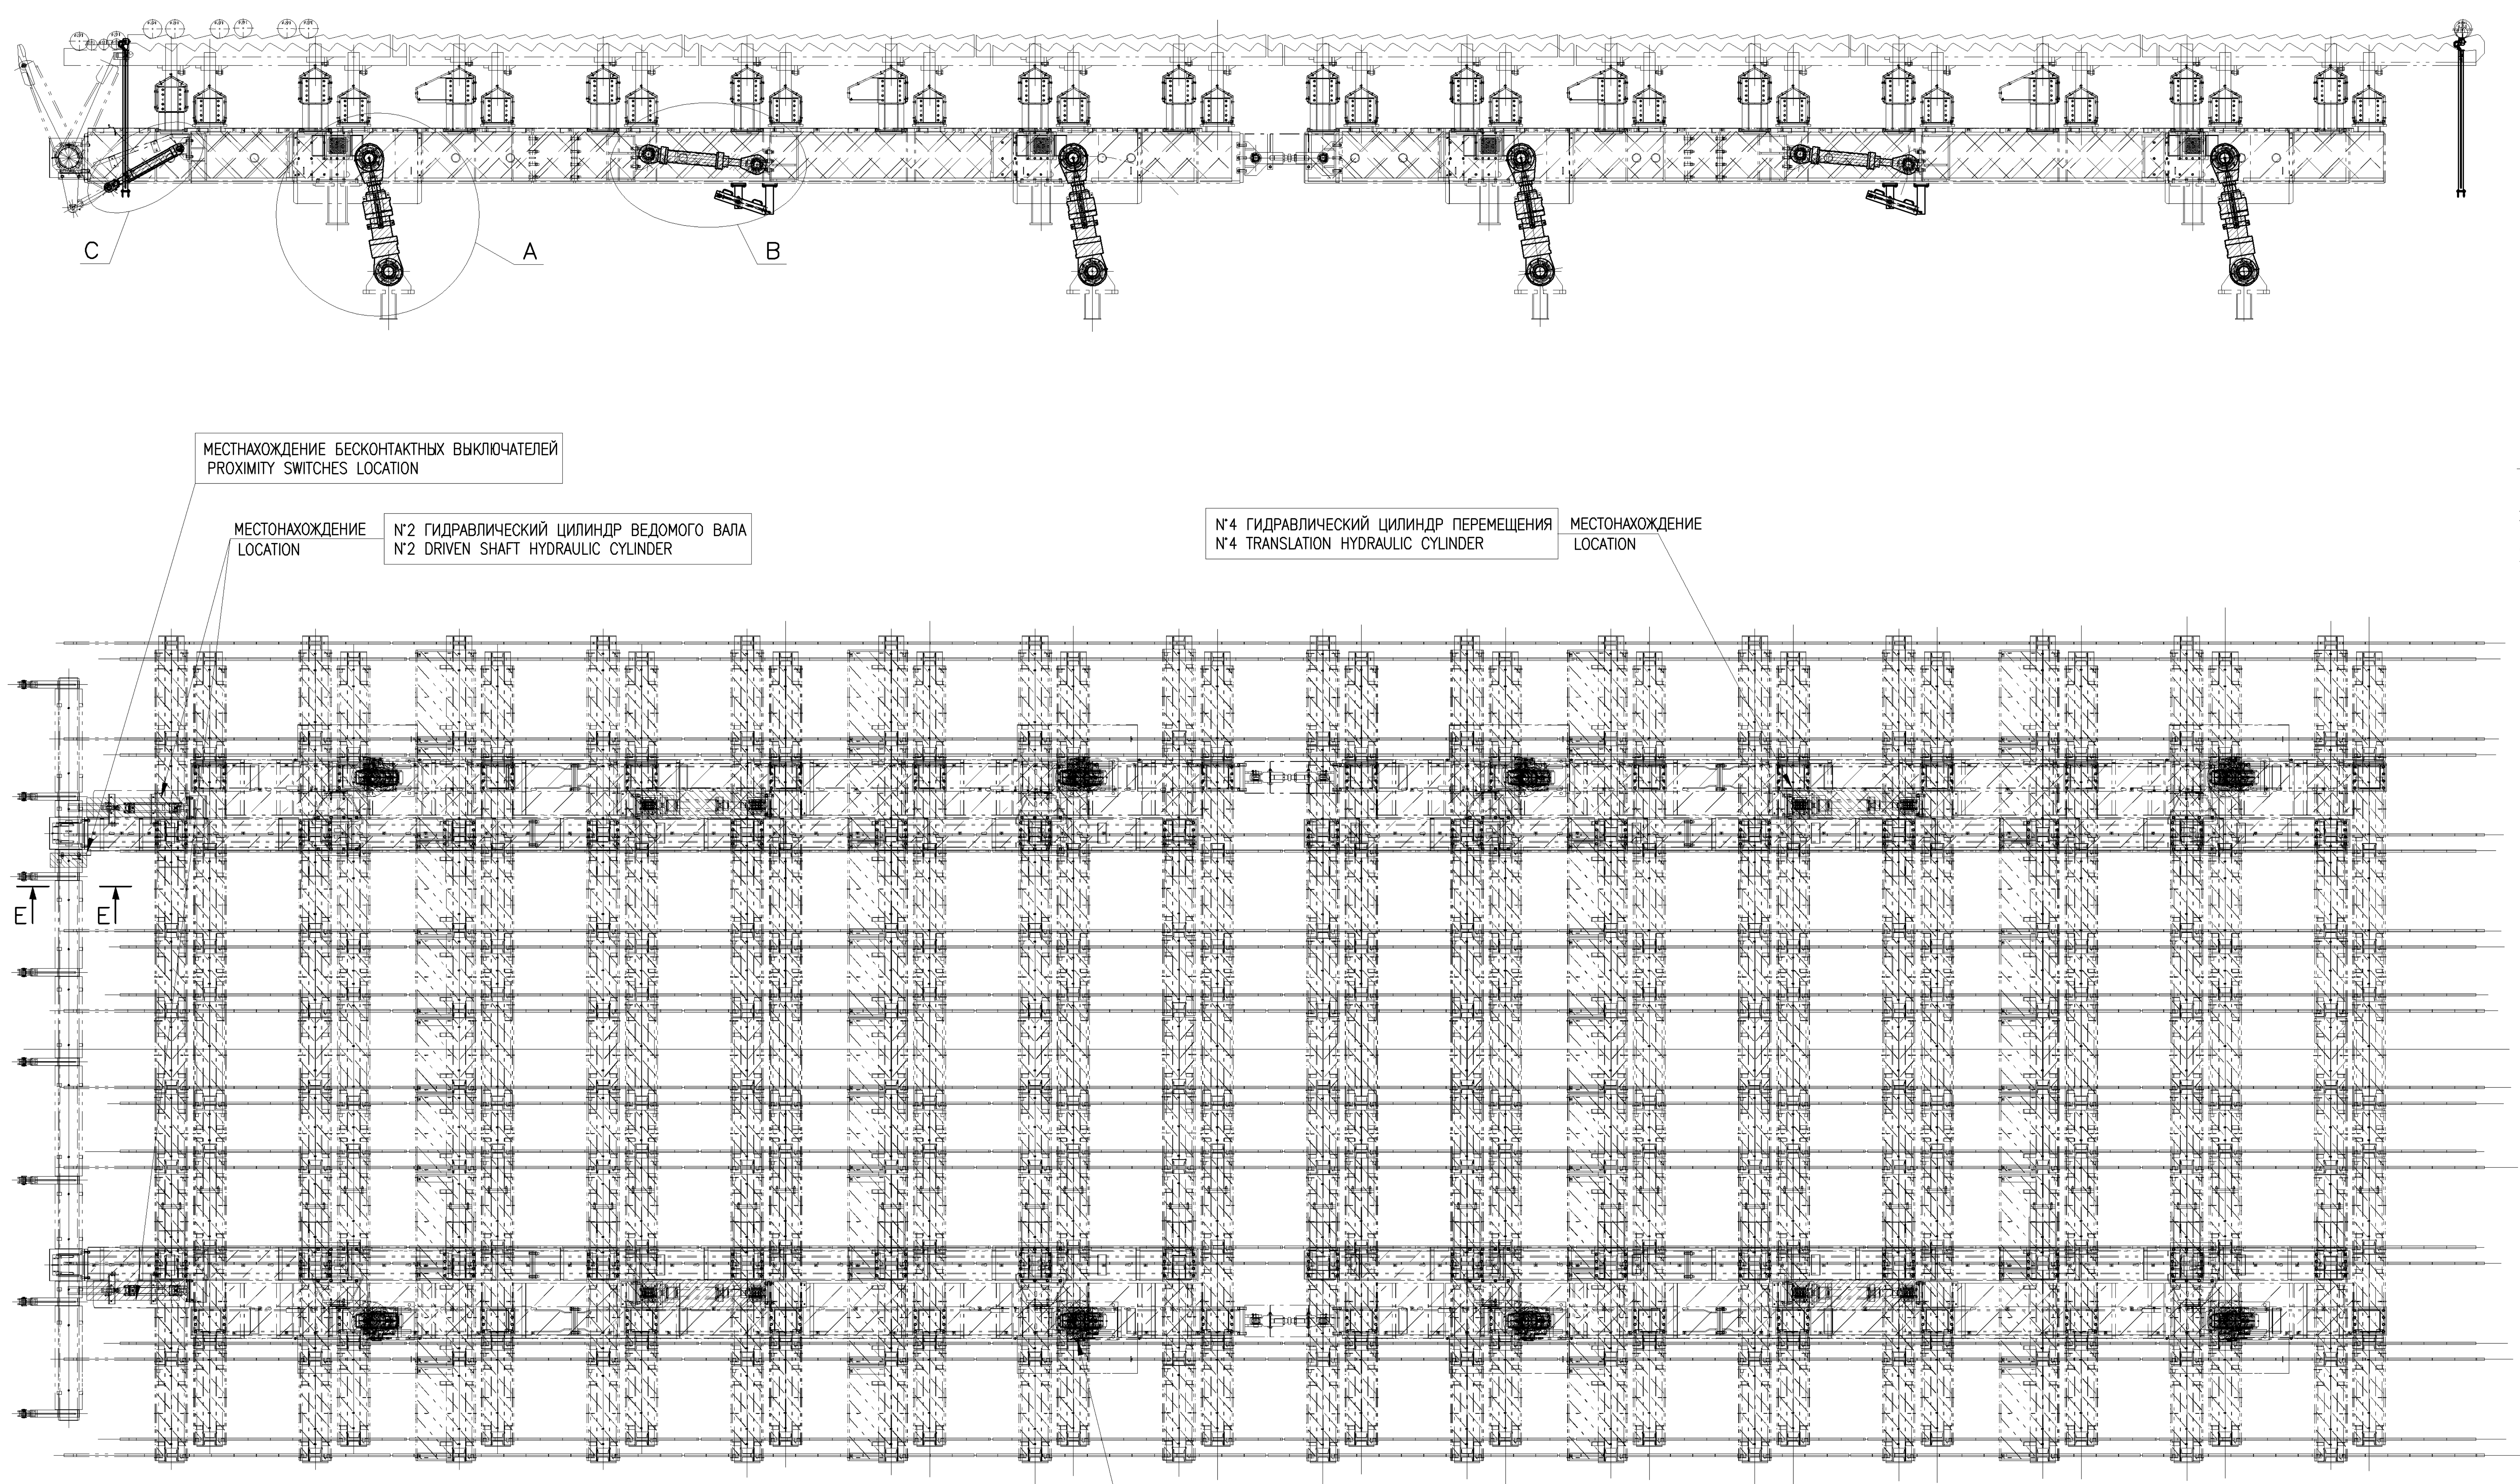
C
A
B
МЕСТНАХОЖДЕНИЕ БЕСКОНТАКТНЫХ ВЫКЛЮЧАТЕЛЕЙ
PROXIMITY SWITCHES LOCATION
МЕСТОНАХОЖДЕНИЕ
LOCATION
N°2 ГИДРАВЛИЧЕСКИЙ ЦИЛИНДР ВЕДОМОГО ВАЛА
N°2 DRIVEN SHAFT HYDRAULIC CYLINDER
N°4 ГИДРАВЛИЧЕСКИЙ ЦИЛИНДР ПЕРЕМЕЩЕНИЯ
N°4 TRANSLATION HYDRAULIC CYLINDER
МЕСТОНАХОЖДЕНИЕ
LOCATION
E
E

МЕСТОНАХОЖДЕНИЕ
LOCATION

N°8 ГИДРАВЛИЧЕСКИЙ ЦИЛИНДР ПОДЪЕМА
N°8 LIFTING HYDRAULIC CYLINDER

ОПТИЧЕСКИЙ ДАТЧИК, СИГНАЛИЗИРУЮЩИЙ ПРИСУТСТВИЕ ЗАГОТОВКИ
OPTICAL SENSOR BILLET PRESENCE SIGNALING

N° 1+1 БЕСКОНТАКТНЫЕ ВЫКЛЮЧАТЕЛИ
ЗАГРУЗОЧНОЕ УСТРОЙСТВО В ПРОДВИНУТОМ ПОЛОЖЕНИИ
ЗАГРУЗОЧНОЕ УСТРОЙСТВО В ОТВЕДЕННОМ ПОЛОЖЕНИИ

N° 1+1 PROXIMITY SWITCHES
CHARGER IN ADVANCE POSITION
CHARGER IN RETRACTED POSITION

E–E
1:10

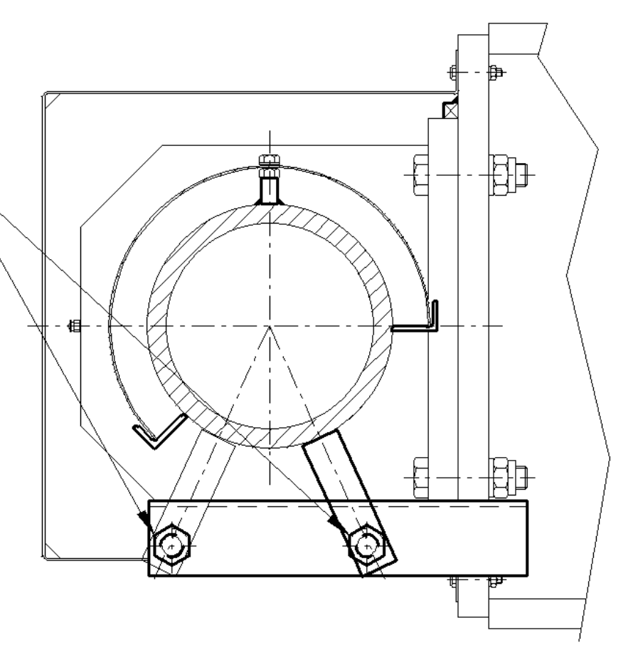

ОПТИЧЕСКИЙ ДАТЧИК, СИГНАЛИЗИРУЮЩИЙ ПРИСУТСТВИЕ ЗАГОТОВКИ
OPTICAL SENSOR BILLET PRESENCE SIGNALING

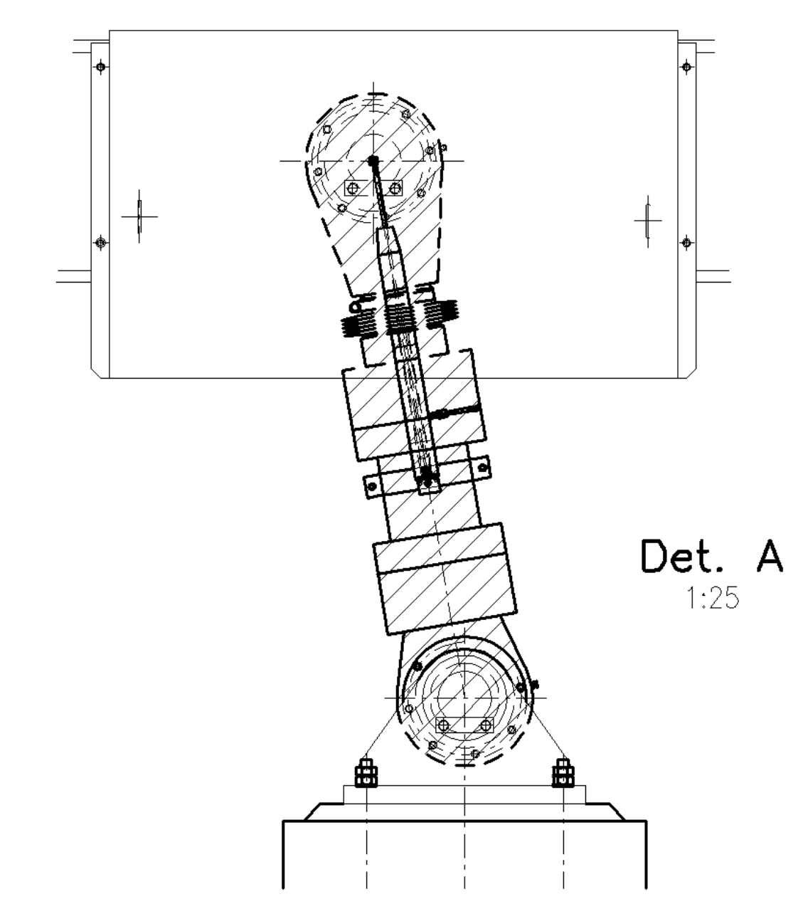

N° 8 HYDRAULIC CYLINDER (LIFTING)
N° 8 ГИДРАВЛИЧЕСКИЙ ЦИЛИНДР (ПОДЪЕМ)

ПОРШЕНЬ: ø280	(PISTON)
ШТОК ПОРШНЯ: ø180	(PISTON ROD)
ХОД:: 325	(STROKE)
РАБОЧЕЕ ДАВЛЕНИЕ: 100 БАР/bar	(WORKING PRESSURE)
ФАКТ. ВРЕМЯ РАБОТЫ–ТОЛКАНИЕ–ТЯГА: 5 сек /sec	(DRIVING TIME–PUSH & PULL)
ТОРМОЖЕНИЕ НА ОБЕИХ СТОРОНАХ: AMBO I LATI	(BRAKING ON BOTH SIDES)

Det. B
1:25

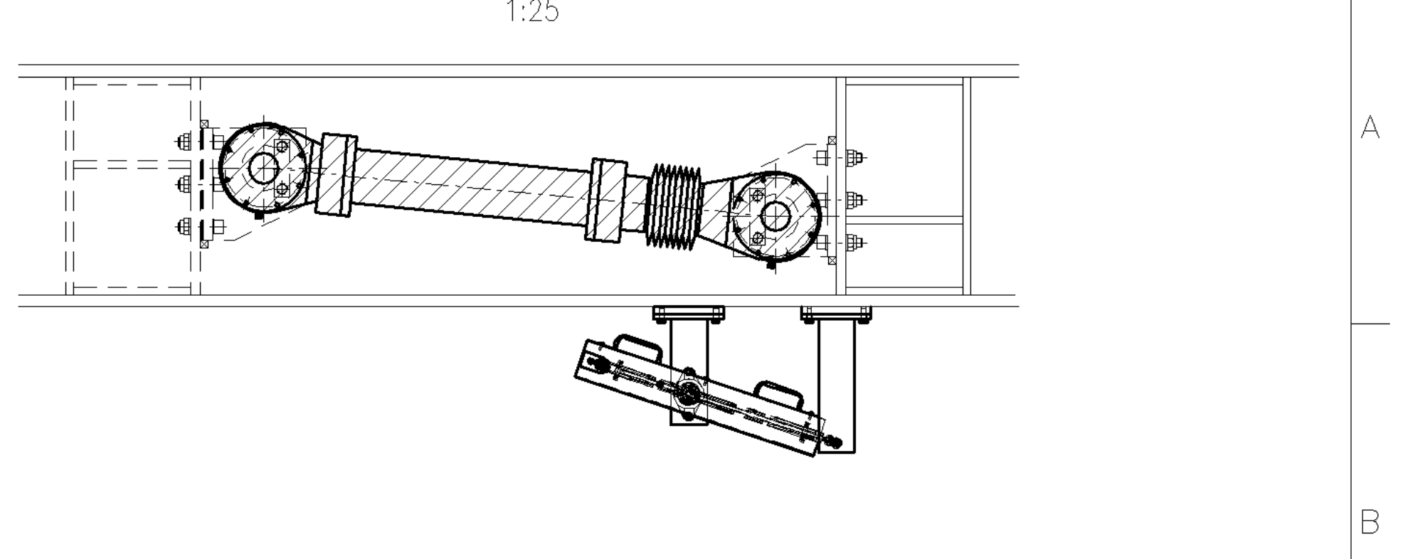

N° 4 HYDRAULIC CYLINDER (TRANSLATION)
N° 4 ГИДРАВЛИЧЕСКИЙ ЦИЛИНДР (ПЕРЕМЕЩЕНИЕ)

ПОРШЕНЬ: ø160	(PISTON)
ШТОК ПОРШНЯ: ø100	(PISTON ROD)
ХОД: 600	(STROKE)
РАБОЧЕЕ ДАВЛЕНИЕ: 100 БАР/bar	(WORKING PRESSURE)
ФАКТ. ВРЕМЯ РАБОТЫ–ТОЛКАНИЕ–ТЯГА: 5 сек /sec	(DRIVING TIME–PUSH & PULL)
ТОРМОЖЕНИЕ НА ОБЕИХ СТОРОНАХ: AMBO I LATI	(BRAKING ON BOTH SIDES)

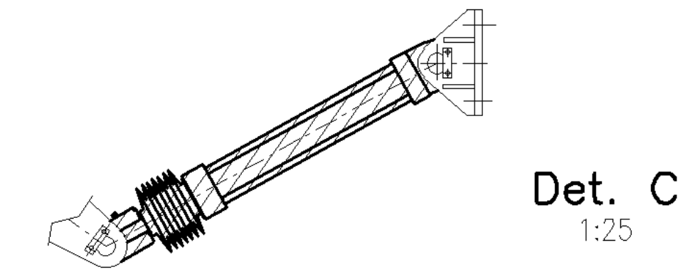

N° 2 HYDRAULIC CYLINDER (DRIVEN SHAFT)
N° 2 ГИДРАВЛИЧЕСКИЙ ЦИЛИНДР (ВЕДОМЫЙ ВАЛ)

ПОРШЕНЬ: ø125	(PISTON)
ШТОК ПОРШНЯ: ø90	(PISTON ROD)
ХОД: 650	(STROKE)
РАБОЧЕЕ ДАВЛЕНИЕ: 130 БАР/bar	(WORKING PRESSURE)
ФАКТ. ВРЕМЯ РАБОТЫ–ТОЛКАНИЕ–ТЯГА: 4 сек /sec	(DRIVING TIME–PUSH & PULL)
ТОРМОЖЕНИЕ НА ОБЕИХ СТОРОНАХ: AMBO I LATI	(BRAKING ON BOTH SIDES)

Rev.	Date	Revisions description	Drawn by	Checked by	Approved by
00	23 Jan 2020	EMISSIONE ISSUED	Bhimered U	Pawar N	Del F

Material 1 (where not indicated on drawing) — State of supply Mat.1 — Danieli Supply Std. — Supply Class — Pattern DB
Material 2 — State of supply Mat.2 — Danieli Supply Std. — Supply Class — Casting Code
Material 1 Equivalent
Heat Treatment
On Drawing Symbol, if required,
Coating
On Drawing Symbol, if required,
Unquoted radius (mm) — Unquoted bevels (mm) — Dimensions without tolerance as per DANIELI STD 2.4.103 — Machinings — Prec.Class — Max. Welding Class
Project Name

DANIELI CENTRO MET

Job nr
Obtained from 6.177795.T
Replaces
Family code/Machine code COMPWI
Weight (Kg)
J (Kgm²)

Title
DEVICE LOCATION

Scale 1:50
Format A1L
Nr. of sheets 001
Sheet 001
Follow

DANIELI Shop number
6.428738.B
Revision 00
DANIELI dwg number
Revision

According to law DANIELI & C. SpA considers this document to be a company secret and therefore prohibits any person to reproduce or disclose it or make it known in whole or in part to other parties or to competitors without specific written authorization of DANIELI's Management

File nr FD12-008-382-254

COP41295-1 DPC13Y023712 B359 8.834046.S

COMPUTER AIDED DESIGN -A