КРУГЛЫЙ/ROUND ø250 – REF. 2 X 6 mt
– REF. 8 mt
– REF. 12 mt
THREE WALKING BEAM CYCLES FOR ONE ROUND
ТРИ ЦИКЛА ШАГАЮЩЕЙ БАЛКИ ДЛЯ ОДНОЙ КРУГЛОЙ ЗАГОТОВКИ

ЭТАП/PHASE 13
КОНЕЦ ЦИКЛА ШАГАЮЩЕЙ БАЛКИ/WALKING BEAM END CYCLE
ЗАМКНУТЫЙ КОНТУР ЦИЛИНДРА ПЕРЕМЕЩЕНИЯ ХОД=415
TRANSLATION CYLINDER CLOSING STROKE=415

ЭТАП/PHASE 12
ОПУСКАНИЕ ШАГАЮЩЕЙ БАЛКИ ХОД = 325
W.B. LOWERING STROKE = 325
ПРИСУТСТВИЕ КРУГА У ФОТОЭЛЕМЕНТА/ROUND PRESENT ON PHOTOCELL | B

ЭТАП/PHASE 11
ОТКРЫТЫЙ КОНТУР ЦИЛИНДРА ПЕРЕМЕЩЕНИЯ ХОД=415
TRANSLATION CYLINDER OPENING STROKE=415

ЭТАП/PHASE 10
НАЧАЛО ЦИКЛА ШАГАЮЩЕЙ БАЛКИ/WALKING BEAM START CYCLE
ОТКРЫТЫЙ КОНТУР ЦИЛИНДРА ПОДЪЕМА ХОД=325
LIFTING CYLINDER OPENING STROKE=325

ЭТАП/PHASE 9
ЗАМКНУТЫЙ КОНТУР ЦИЛИНДРА ПЕРЕМЕЩЕНИЯ ХОД=415
TRANSLATION CYLINDER CLOSING STROKE=415

ЭТАП/PHASE 8
ОПУСКАНИЕ ШАГАЮЩЕЙ БАЛКИ ХОД = 325
W.B. LOWERING STROKE = 325

ЭТАП/PHASE 7
ОТКРЫТЫЙ КОНТУР ЦИЛИНДРА ПЕРЕМЕЩЕНИЯ ХОД=415
TRANSLATION CYLINDER OPENING STROKE=415

ЭТАП/PHASE 6
НАЧАЛО ЦИКЛА ШАГАЮЩЕЙ БАЛКИ/WALKING BEAM START CYCLE
ОТКРЫТЫЙ КОНТУР ЦИЛИНДРА ПОДЪЕМА ХОД=325
LIFTING CYLINDER OPENING STROKE=325

ЭТАП/PHASE 5
КОНЕЦ ЦИКЛА ШАГАЮЩЕЙ БАЛКИ/WALKING BEAM END CYCLE
ЗАМКНУТЫЙ КОНТУР ЦИЛИНДРА ПЕРЕМЕЩЕНИЯ ХОД=415
TRANSLATION CYLINDER CLOSING STROKE=415


ЭТАП/PHASE 4
ОПУСКАНИЕ ШАГАЮЩЕЙ БАЛКИ ХОД = 325
W.B. LOWERING STROKE = 325

ЭТАП/PHASE 3
ОТКРЫТЫЙ КОНТУР ЦИЛИНДРА ПЕРЕМЕЩЕНИЯ ХОД=415
TRANSLATION CYLINDER OPENING STROKE=415

ЭТАП/PHASE 2
НАЧАЛО ЦИКЛА ШАГАЮЩЕЙ БАЛКИ/WALKING BEAM START CYCLE
ОТКРЫТЫЙ КОНТУР ЦИЛИНДРА ПОДЪЕМА ХОД=325
LIFTING CYLINDER OPENING STROKE=325

ЭТАП/PHASE 1
ОТКРЫТЫЙ КОНТУР ЦИЛИНДРА ВАЛА УПРАВЛЕНИЯ ХОД=650
CONTROL SHAFT CYLINDER OPENING STROKE=650
ПРИСУТСТВИЕ КРУГА У ФОТОЭЛЕМЕНТА/ROUND PRESENT ON PHOTOCELL | A

СОСТОЯНИЕ ШАГАЮЩЕЙ БАЛКИ ДЛЯ НАЧАЛА ЦИКЛА
WALKING BEAM SITUATION FOR START CYCLE
ЗАМКНУТЫЙ КОНТУР ЦИЛИНДРА ПЕРЕМЕЩЕНИЯ ШАГАЮЩЕЙ БАЛКИ
WALKING BEAM TRANSLATION CYLINDER CLOSED
ЗАМКНУТЫЙ КОНТУР ЦИЛИНДРА ПОДЪЕМА ШАГАЮЩЕЙ БАЛКИ
WALKING BEAM LIFTING CYLINDER CLOSED

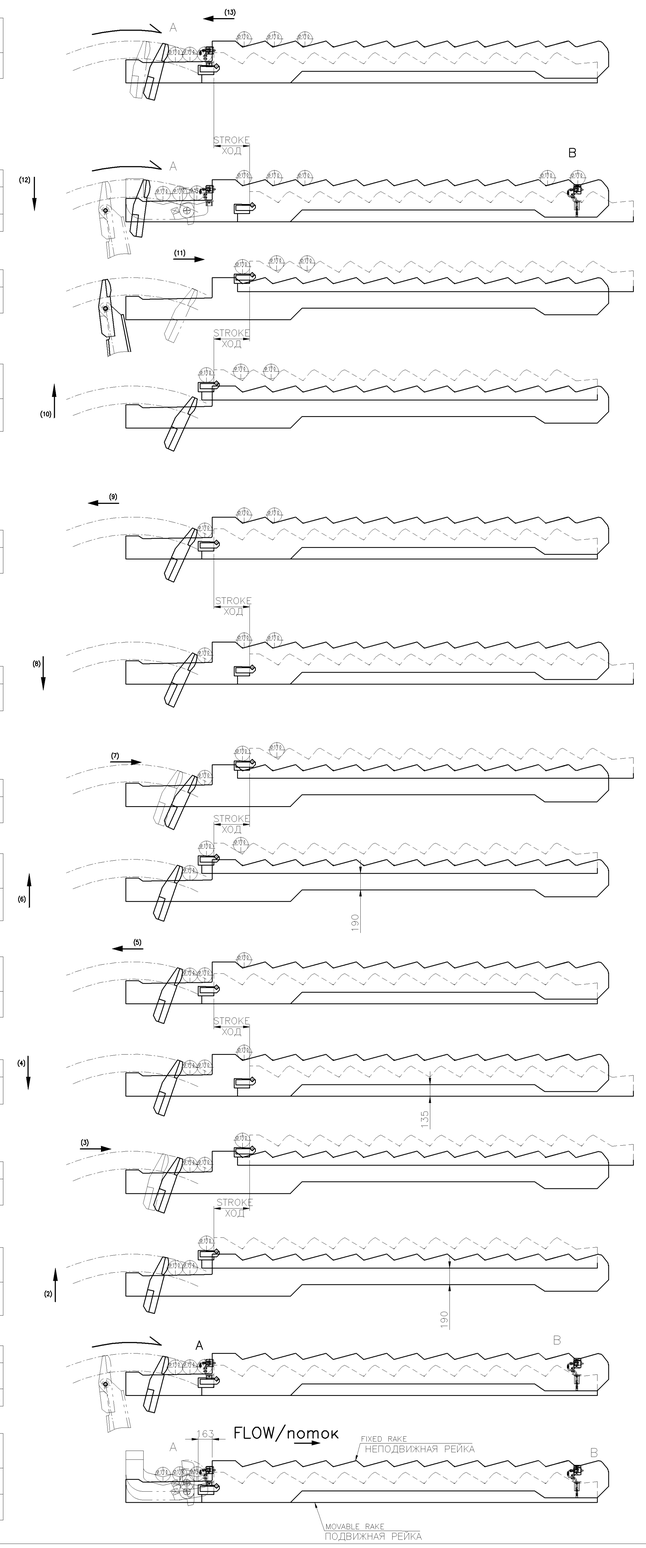

Rev.	Date	Revisions description	Drawn by	Checked by	Approved by
00	29 Jan 2020	EMISSIONE ISSUED	Ekimenkova U	Power N	Del F

Material 1 (where not indicated on drawing) | State of supply Mat.1 | Danieli Supply Std. | Supply Class | Pattern DB
Material 2 | State of supply Mat.2 | Danieli Supply Std. | Supply Class | Casting Code
Material 1 Equivalent
Heat Treatment
On Drawing Symbol, if required,
Coating
On Drawing Symbol, if required,
Unquoted radius (mm) | Unquoted bevels (mm) | Dimensions without tolerance as per DANIELI STD 2.4.103 | Machinings | Prec.Class | Max. Welding Class
Project Name

DANIELI CENTRO MET

Job nr
Obtained from 6.177794.S
Replaces
Family code/Machine code COMpwi
Weight (Kg) | J (Kgm²)

Title
MOTION DIAGRAM

DANIELI Shop number 6.428744.G | Revision 00
DANIELI dwg number | Revision
Scale 1:25
Format A0
Nr. of sheets 002
Sheet 002 | Follow

According to law DANIELI & C. SpA considers this document to be a company secret and therefore prohibits any person to reproduce or disclose it or make it known in whole or in part to other parties or to competitors without specific written authorization of DANIELI's Management.

File nr FD12-012-129-121

COMPUTER AIDED DESIGN -A

B861 8.83046.S
COP41295-1 DPC13702312