КРУГЛЫЙ/ROUND ⌀290 – REF. 2 X 6 mt
– REF. 8 mt
– REF. 12 mt
TWO WALKING BEAM CYCLES FOR ONE ROUND
ДВА ЦМКЛА ШАГАЮЩЕЙ БАЛКИ ДЛЯ ОДНОЙ КРУГЛОЙ ЗАГОТОВКИ

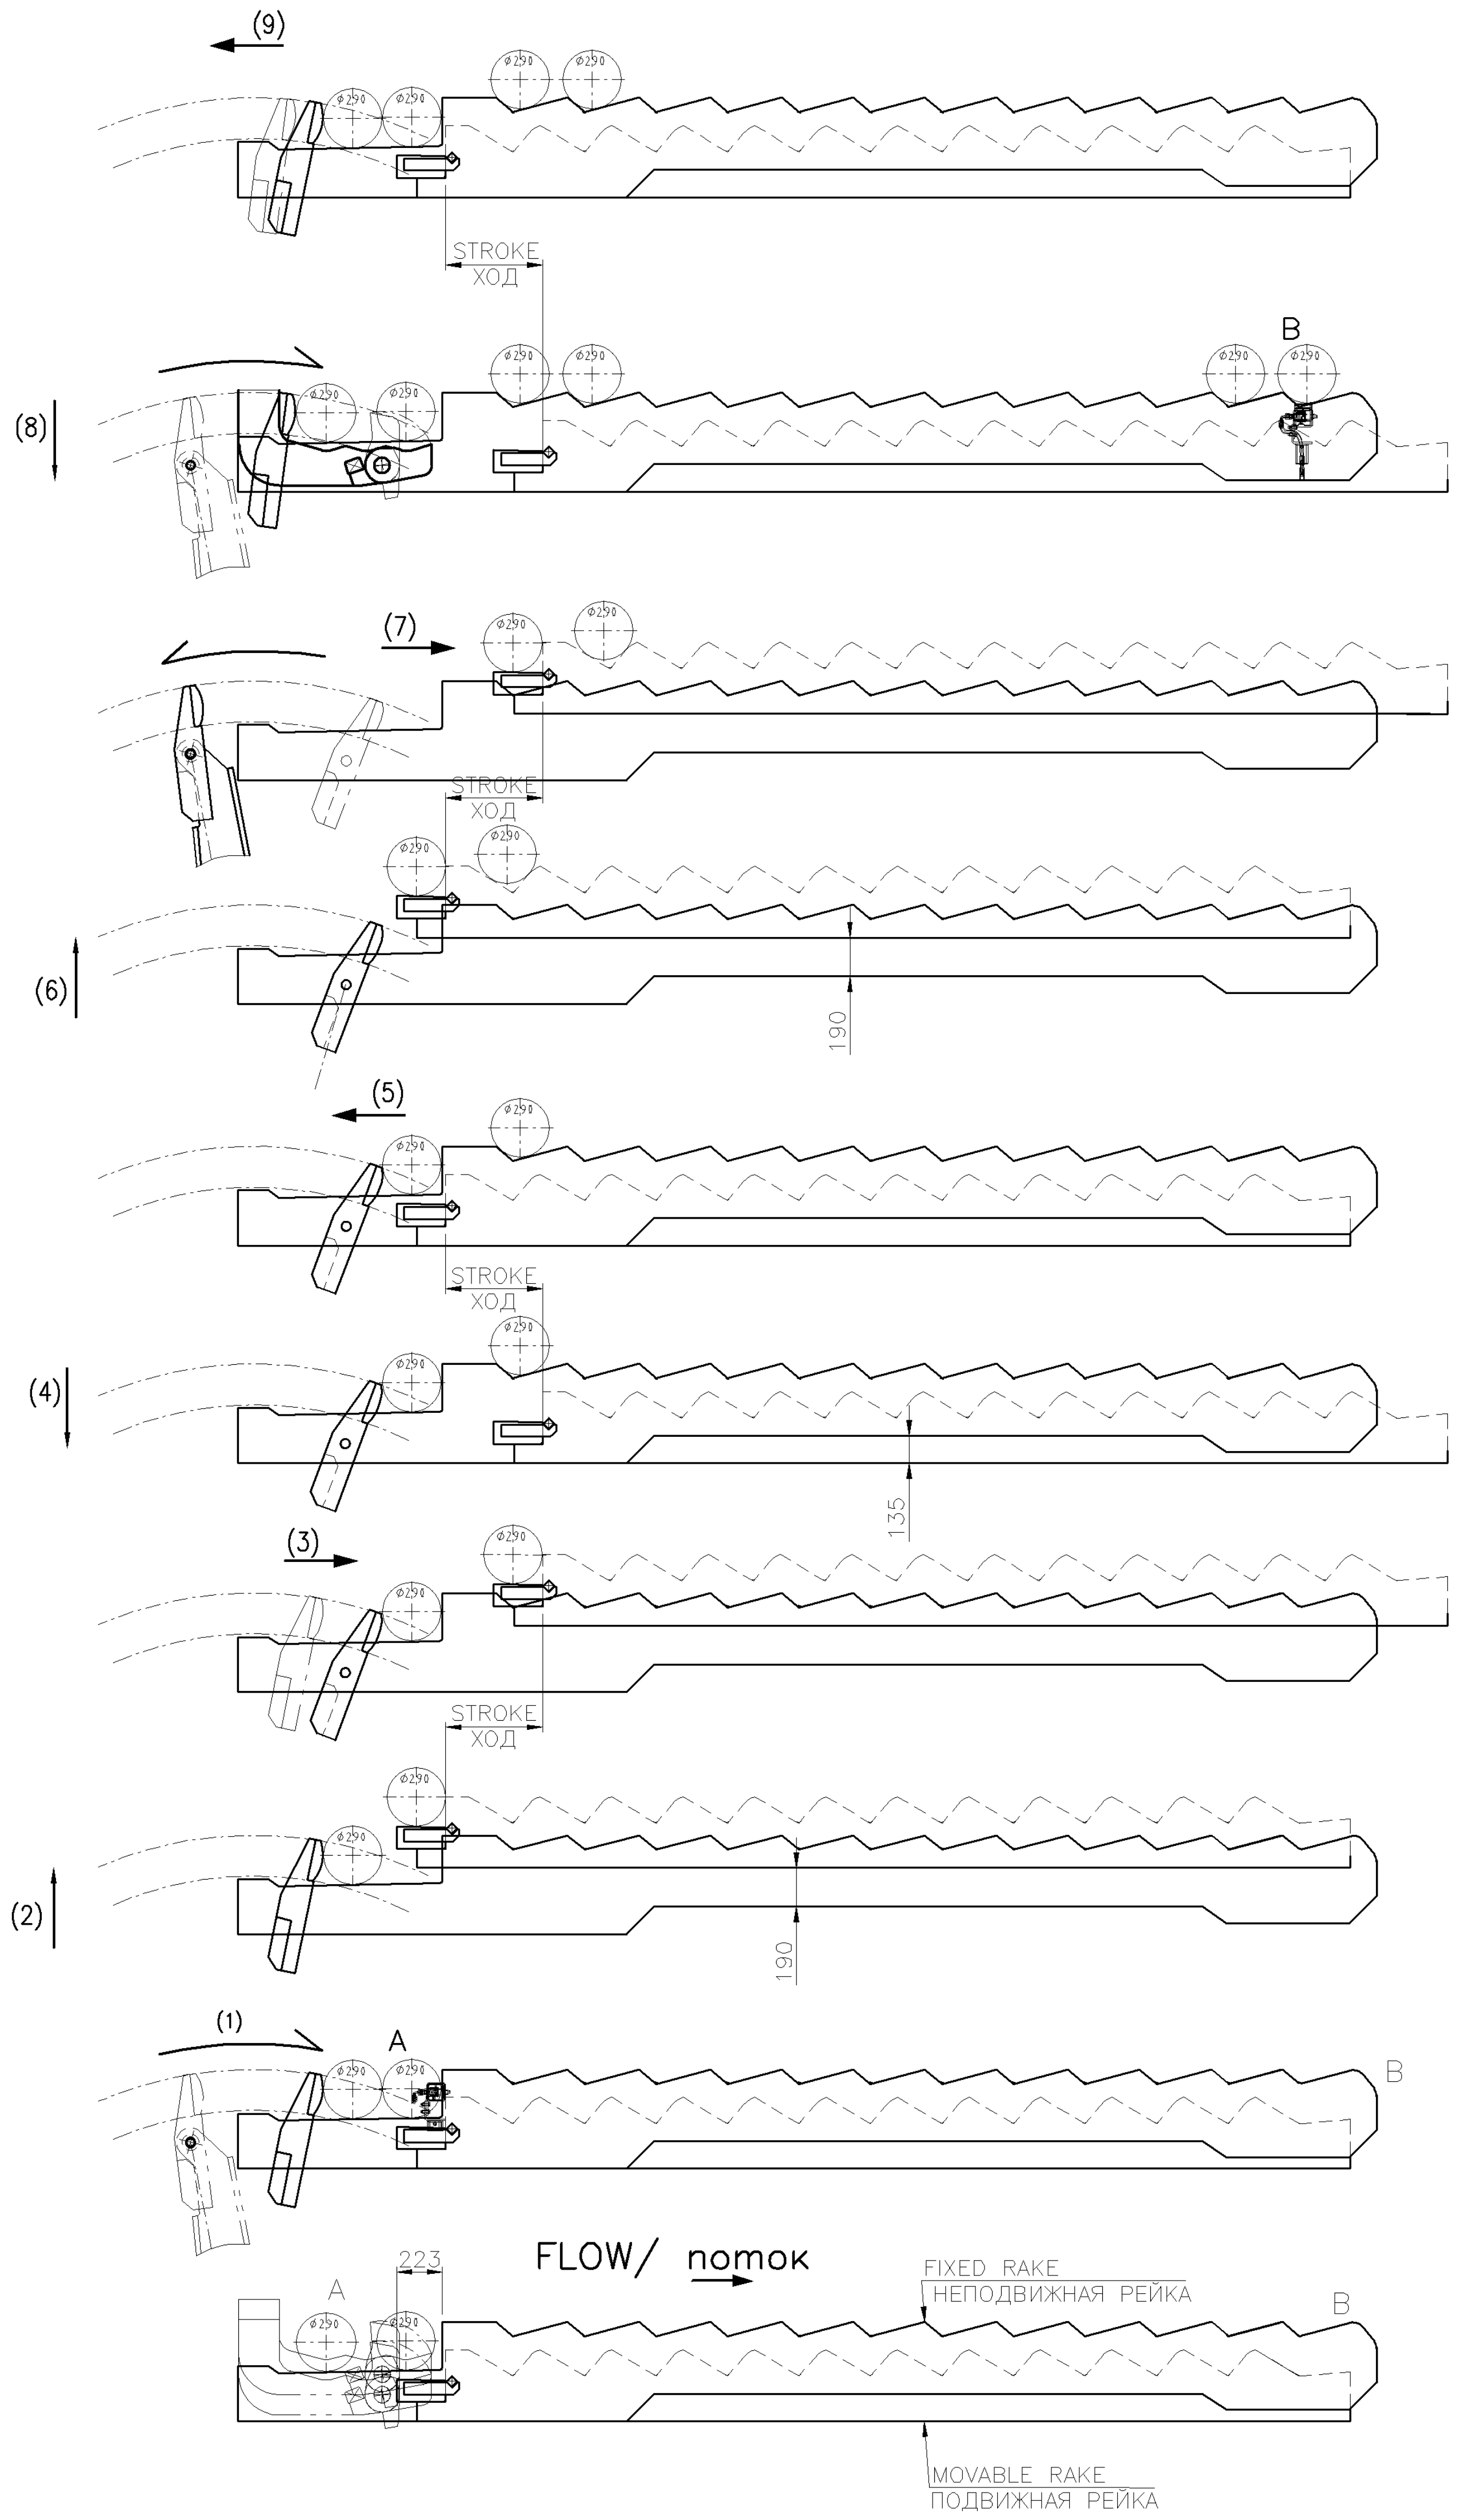

ЭТАП/PHASE 9
КОНЕЦ ЦИКЛА ШАГАЮЩЕЙ БАЛКИ/WALKING BEAM END CYCLE
ЗАМКНУТЫЙ КОНТУР ЦИЛИНДРА ПЕРЕМЕЩЕНИЯ ХОД=475
TRANSLATION CYLINDER CLOSING STROKE=475

ЭТАП/PHASE 8
ОПУСКАНИЕ ШАГАЮЩЕЙ БАЛКИ ХОД= 325
W.B. LOWERING STROKE = 325
ПРИСУТСТВИЕ КРУГА У ФОТОЭЛЕМЕНТА/ROUND PRESENT ON PHOTOCELL B

ЭТАП/PHASE 7
ОТКРЫТЫЙ КОНТУР ЦИЛИНДРА ПЕРЕМЕЩЕНИЯ ХОД=475
TRANSLATION CYLINDER OPENING STROKE=475

ЭТАП/PHASE 6
НАЧАЛО ЦИКЛА ШАГАЮЩЕЙ БАЛКИ/WALKING BEAM START CYCLE
ОТКРЫТЫЙ КОНТУР ЦИЛИНДРА ПОДЪЕМА ХОД=325
LIFTING CYLINDER OPENING STROKE=325

ЭТАП/PHASE 5
КОНЕЦ ЦИКЛА ШАГАЮЩЕЙ БАЛКИ/WALKING BEAM END CYCLE
ЗАМКНУТЫЙ КОНТУР ЦИЛИНДРА ПЕРЕМЕЩЕНИЯ ХОД=475
TRANSLATION CYLINDER CLOSING STROKE=475

ЭТАП/PHASE 4
ОПУСКАНИЕ ШАГАЮЩЕЙ БАЛКИ ХОД = 325
W.B. LOWERING STROKE = 325

ЭТАП/PHASE 3
ОТКРЫТЫЙ КОНТУР ЦИЛИНДРА ПЕРЕМЕЩЕНИЯ ХОД=475
TRANSLATION CYLINDER OPENING STROKE=475

ЭТАП/PHASE 2
НАЧАЛО ЦИКЛА ШАГАЮЩЕЙ БАЛКИ/WALKING BEAM START CYCLE
ОТКРЫТЫЙ КОНТУР ЦИЛИНДРА ПОДЪЕМА ХОД=325
LIFTING CYLINDER OPENING STROKE=325

ЭТАП/PHASE 1
ОТКРЫТЫЙ КОНТУР ЦИЛИНДРА ВАЛА УПРАВЛЕНИЯ ХОД=650
CONTROL SHAFT CYLINDER OPENING STROKE=650
ПРИСУТСТВИЕ КРУГА У ФОТОЭЛЕМЕНТА/ROUND PRESENT ON PHOTOCELL A

СОСТОЯНИЕ ШАГАЮЩЕЙ БАЛКИ ДЛЯ НАЧАЛА ЦИКЛА
WALKING BEAM SITUATION FOR START CYCLE
ЗАМКНУТЫЙ КОНТУР ЦИЛИНДРА ПЕРЕМЕЩЕНИЯ ШАГАЮЩЕЙ БАЛКИ
WALKING BEAM TRANSLATION CYLINDER CLOSED
ЗАМКНУТЫЙ КОНТУР ЦИЛИНДРА ПОДЪЕМА ШАГАЮЩЕЙ БАЛКИ
WALKING BEAM LIFTING CYLINDER CLOSED

ЭТАП/PHASE 9
КОНЕЦ ЦИКЛА ШАГАЮЩЕЙ БАЛКИ/WALKING BEAM END CYCLE
ЗАМКНУТЫЙ КОНТУР ЦИЛИНДРА ПЕРЕМЕЩЕНИЯ ХОД=455
TRANSLATION CYLINDER CLOSING STROKE=455

ЭТАП/PHASE 8
ОПУСКАНИЕ ШАГАЮЩЕЙ БАЛКИ ХОД = 325
W.B. LOWERING STROKE = 325
ПРИСУТСТВИЕ КРУГА У ФОТОЭЛЕМЕНТА/ROUND PRESENT ON PHOTOCELL B

ЭТАП/PHASE 7
ОТКРЫТЫЙ КОНТУР ЦИЛИНДРА ПЕРЕМЕЩЕНИЯ ХОД=455
TRANSLATION CYLINDER OPENING STROKE=455

ЭТАП/PHASE 6
НАЧАЛО ЦИКЛА ШАГАЮЩЕЙ БАЛКИ/WALKING BEAM START CYCLE
ОТКРЫТЫЙ КОНТУР ЦИЛИНДРА ПОДЪЕМА ХОД=325
LIFTING CYLINDER OPENING STROKE=325

ЭТАП/PHASE 5
КОНЕЦ ЦИКЛА ШАГАЮЩЕЙ БАЛКИ/WALKING BEAM END CYCLE
ЗАМКНУТЫЙ КОНТУР ЦИЛИНДРА ПЕРЕМЕЩЕНИЯ ХОД=455
TRANSLATION CYLINDER CLOSING STROKE=455

ЭТАП/PHASE 4
ОПУСКАНИЕ ШАГАЮЩЕЙ БАЛКИ ХОД = 325
W.B. LOWERING STROKE = 325

ЭТАП/PHASE 3
ОТКРЫТЫЙ КОНТУР ЦИЛИНДРА ПЕРЕМЕЩЕНИЯ ХОД=455
TRANSLATION CYLINDER OPENING STROKE=455

ЭТАП/PHASE 2
НАЧАЛО ЦИКЛА ШАГАЮЩЕЙ БАЛКИ/WALKING BEAM START CYCLE
ОТКРЫТЫЙ КОНТУР ЦИЛИНДРА ПОДЪЕМА ХОД=325
LIFTING CYLINDER OPENING STROKE=325

ЭТАП/PHASE 1
ОТКРЫТЫЙ КОНТУР ЦИЛИНДРА ВАЛА УПРАВЛЕНИЯ ХОД=650
CONTROL SHAFT CYLINDER OPENING STROKE=650
ПРИСУТСТВИЕ КРУГА У ФОТОЭЛЕМЕНТА/ROUND PRESENT ON PHOTOCELL A

СОСТОЯНИЕ ШАГАЮЩЕЙ БАЛКИ ДЛЯ НАЧАЛА ЦИКЛА
WALKING BEAM SITUATION FOR START CYCLE
ЗАМКНУТЫЙ КОНТУР ЦИЛИНДРА ПЕРЕМЕЩЕНИЯ ШАГАЮЩЕЙ БАЛКИ
WALKING BEAM TRANSLATION CYLINDER CLOSED
ЗАМКНУТЫЙ КОНТУР ЦИЛИНДРА ПОДЪЕМА ШАГАЮЩЕЙ БАЛКИ
WALKING BEAM LIFTING CYLINDER CLOSED

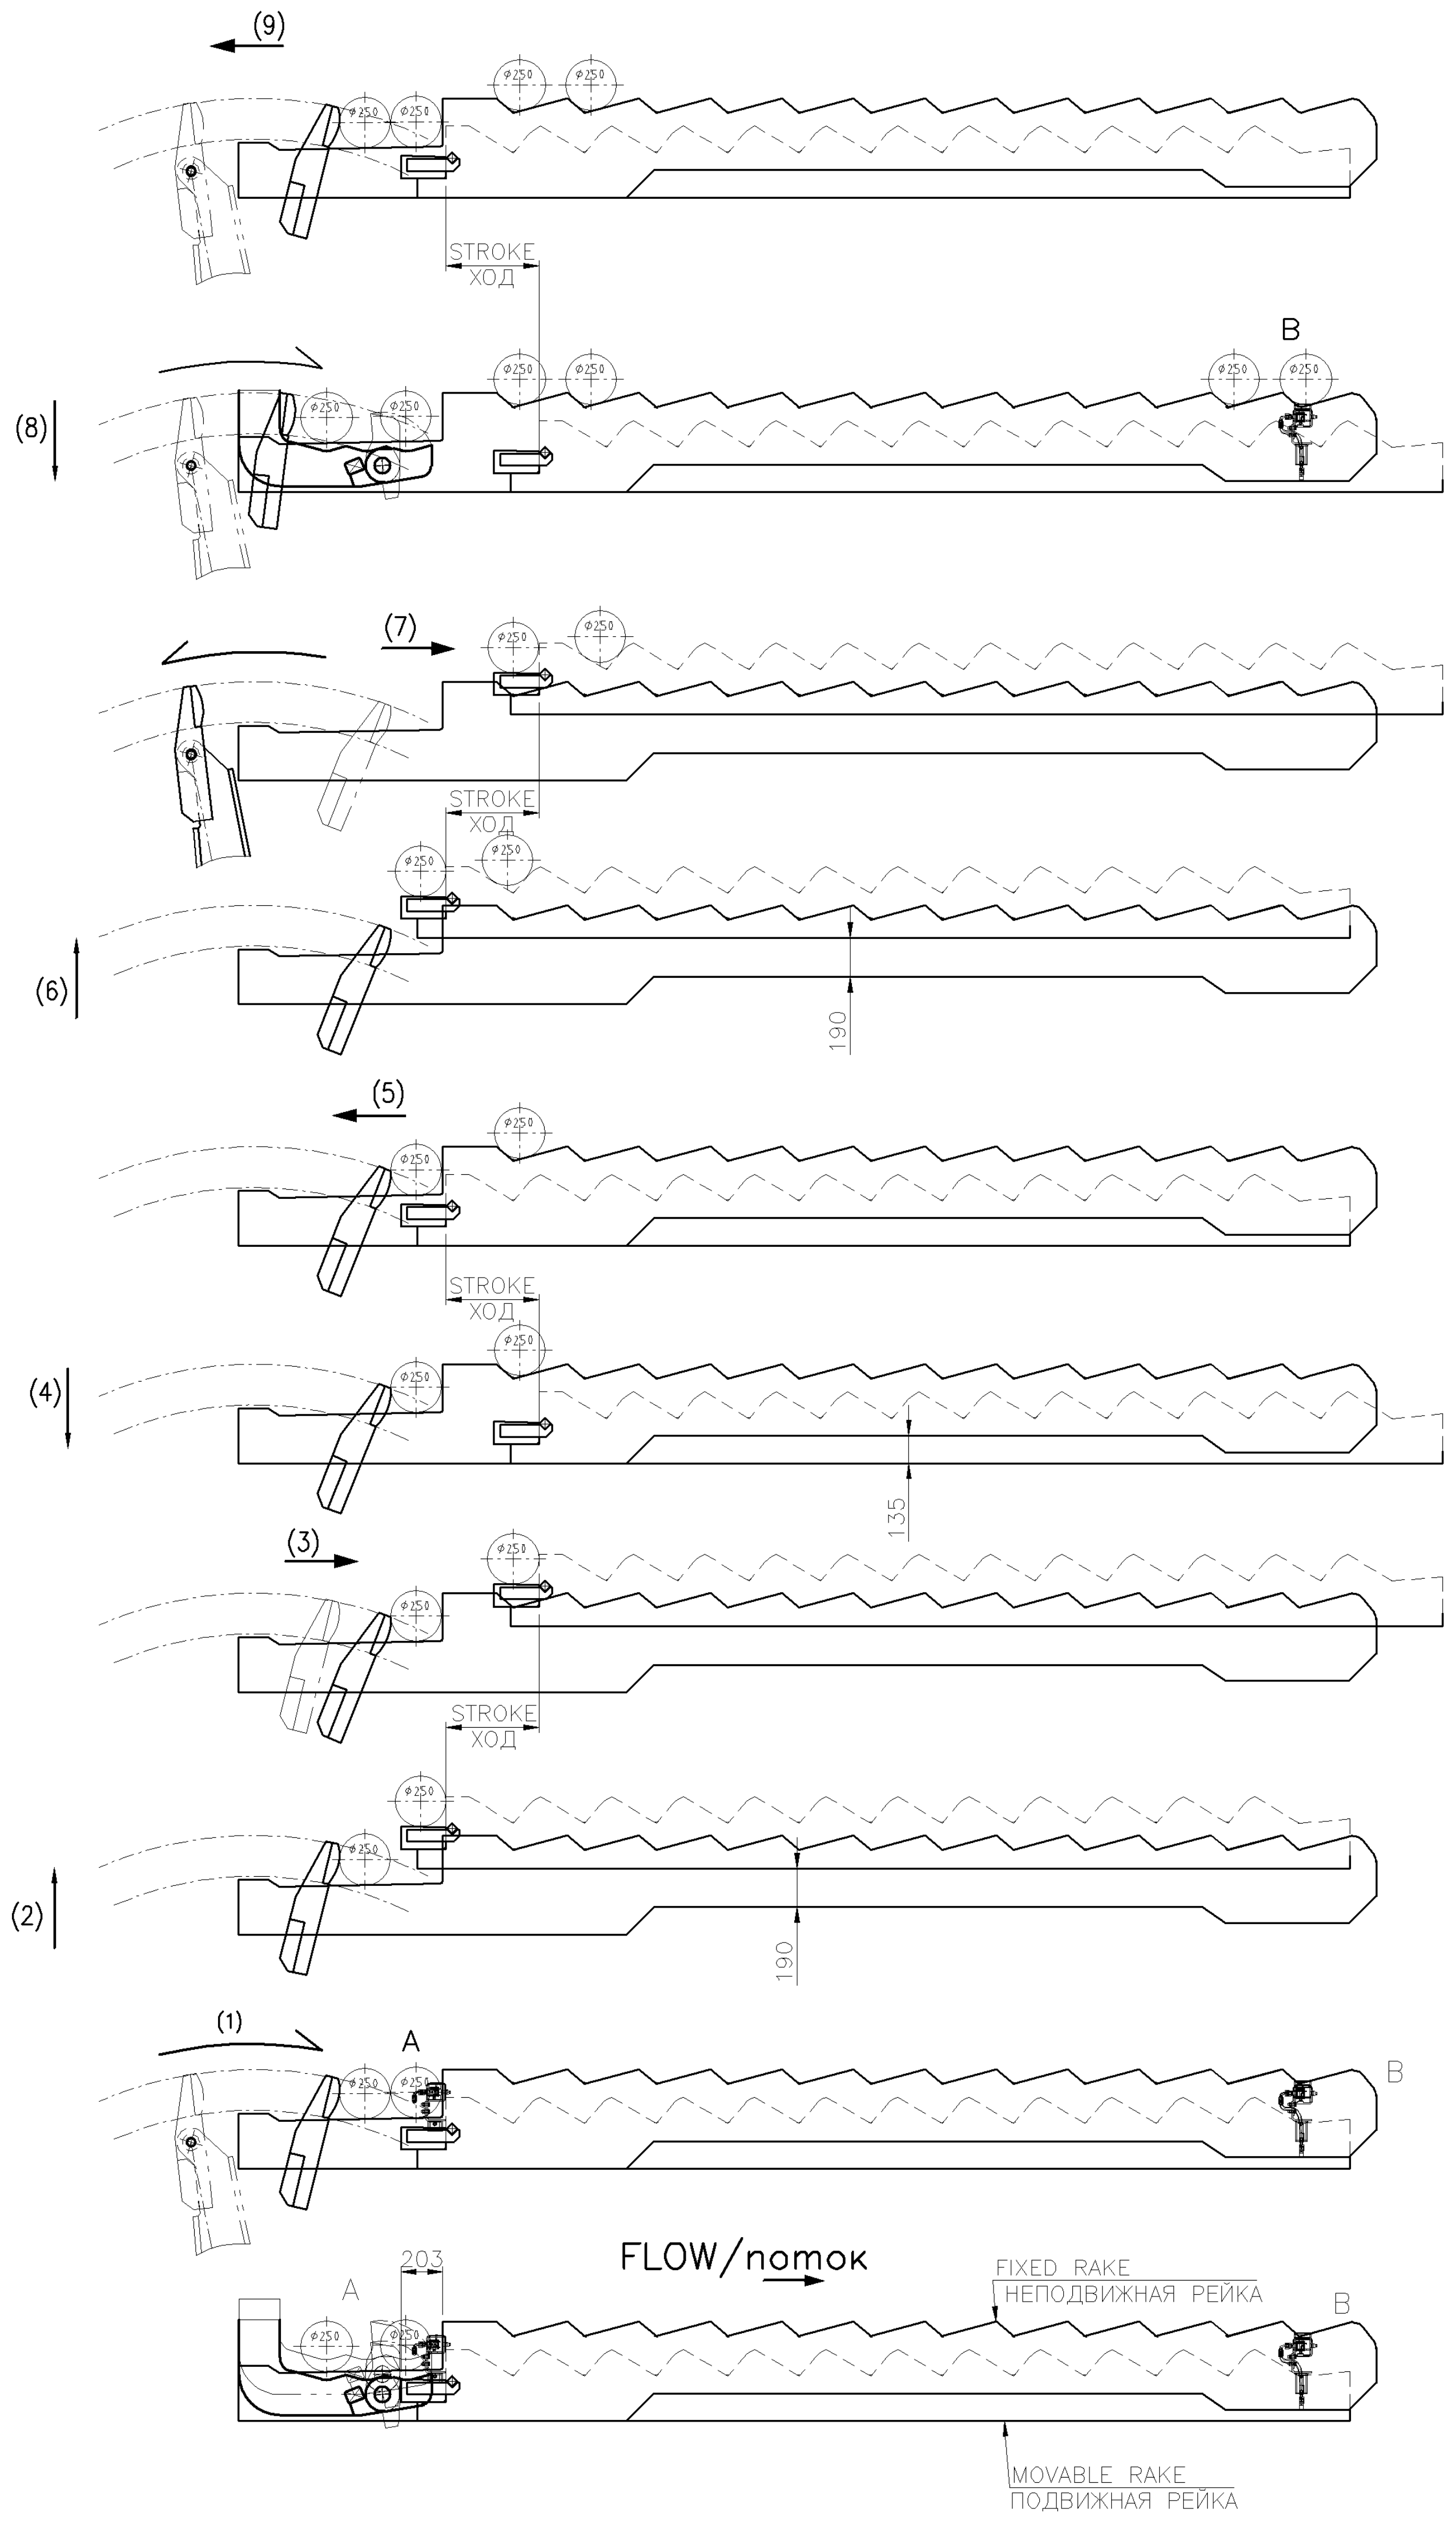

КРУГЛЫЙ/ROUND ⌀250 – REF. 2 X 6 mt
– REF. 8 mt
– REF. 12 mt
TWO WALKING BEAM CYCLES FOR ONE ROUND
ДВА ЦМКЛА ШАГАЮЩЕЙ БАЛКИ ДЛЯ ОДНОЙ КРУГЛОЙ ЗАГОТОВКИ

MAX WALKING BEAM CAPACITY = 660 t
МАКС. ПРОИЗВОДИТЕЛЬНОСТЬ ШАГАЮЩЕЙ БАЛКИ

Rev.	Date	Revisions description	Drawn by	Checked by	Approved by
00	29 Jan 2020	EMISSIONE ISSUED	Bhimered U	Pawar N	Del F

Material 1 (where not indicated on drawing) — State of supply Mat.1 — Danieli Supply Std. — Supply Class — Pattern DB
Material 2 — State of supply Mat.2 — Danieli Supply Std. — Supply Class — Casting Code
Material 1 Equivalent
Heat Treatment
On Drawing Symbol, if required,
Coating
On Drawing Symbol, if required,
Unquoted radius (mm) — Unquoted bevels (mm) — Dimensions without tolerance as per DANIELI STD 2.4.103 — Machinings — Prec.Class — Max. Welding Class
Project Name

DANIELI CENTRO MET

Job nr
Obtained from 6.177794.S
Replaces
Family code/Machine code COMpwi
Weight (Kg)
J (Kgm²)

Title
MOTION DIAGRAM

Scale 1:25
Format A0
Nr. of sheets 002
Sheet 001
Follow

DANIELI Shop number
6.428744.G
Revision 00
DANIELI dwg number
Revision

According to law DANIELI & C. SpA considers this document to be a company secret and therefore prohibits any person to reproduce or disclose it or make it known in whole or in part to other parties or to competitors without specific written authorization of DANIELI's Management

File nr FD12-012-129-093

COP41295-1 Q DPC13Y023712 B361 8.834046.S

COMPUTER AIDED DESIGN -A