




A (1 : 20)
TYP.FOR LIFTING.LOWING .CYLINDER
ОБЫЧНЫЙ ЦИЛИНДР ДЛЯ ПОДЪЕМА И ОПУСКАНИЯ

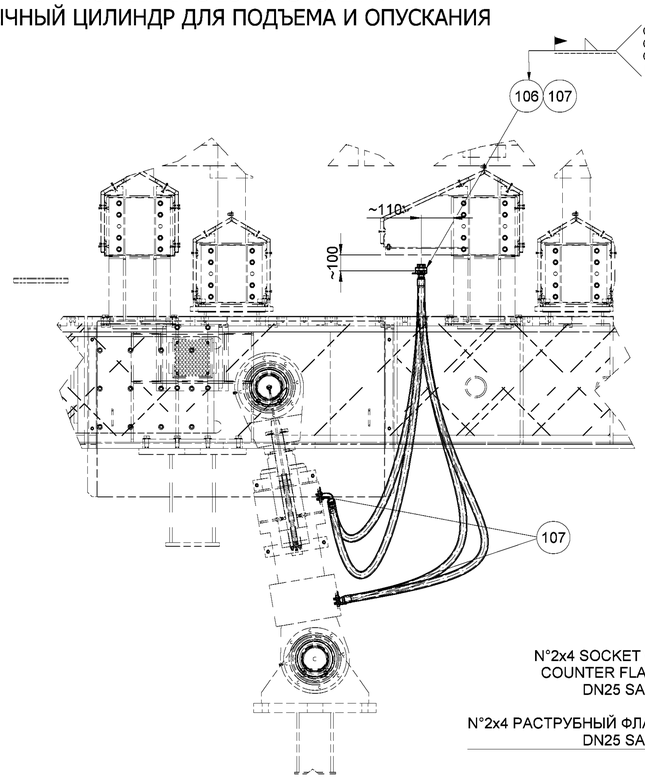


B (1 : 20)
TYP.FOR ADV/RET .CYLINDER

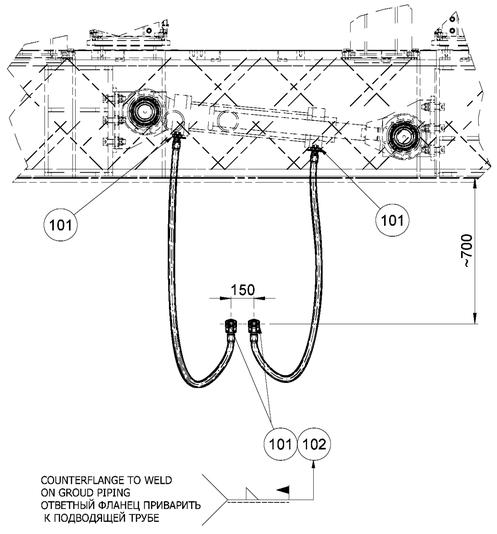

D (1 : 20)

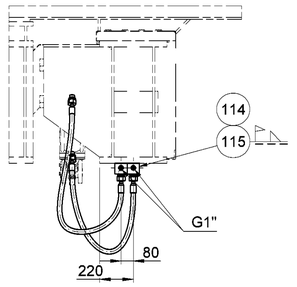


C (1 : 20)
TYP.FEEDING .CLINDER
ОБЫЧНЫЙ ПОДАЮЩИЙ ЦИЛИНДР

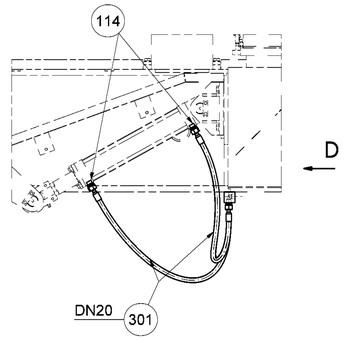


N°2x4 SOCKET WELD
COUNTER FLANCES
DN25 SAE3000

N°2x4 РАСТРУБНЫЙ ФЛАНЕЦ
DN25 SAE3000

AXONOMETRIC VIEW

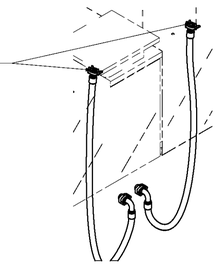

AXONOMETRIC VIEW

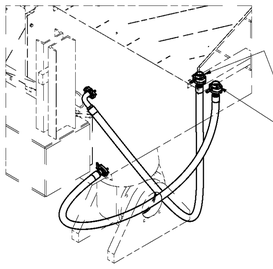

N°2x8 SOCKET WELD
COUNTER FLANCES
DN32 SAE3000


N°2x8 РАСТРУБНЫЙ ФЛАНЕЦ
DN32 SAE3000

NOTE: ASSEMBLY FITTINGS, PIPES AND VALVE
ON THE CYLINDER ON WORKSHOP BUT
DISPATCH SEPARATELY

ПРИМЕЧАНИЕ: СБОРКА СОЕДИНИТЕЛЬНЫХ
ЧАСТЕЙ, ТРУБ И КЛАПАНОВ НА ЦИЛИНДР
ОСУЩЕСТВЛЯЕТСЯ В ЦЕХЕ,
НО ОТПРАВЛЯЕТСЯ ОТДЕЛЬНО


ASSEMBLY SCHEME FOR HOSE ANTIEXTRACTION SYSTEM DN20
FOR SOCKET TYPE HOSE

СХЕМА СБОРКИ ДЛЯ СИСТЕМЫ ПРОТИВОИЗВЛЕЧЕНИЯ ШЛАНГОВ DN20
ДЛЯ ШТЫРЕВЫХ ШЛАНГОВ

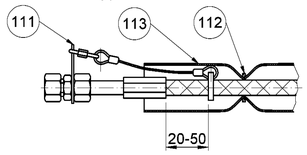


ASSEMBLY SCHEME FOR HOSE ANTIEXTRACTION SYSTEM DN25
FOR SAE FLANGE TYPE HOSE

СХЕМА СБОРКИ ДЛЯ СИСТЕМЫ ПРОТИВОИЗВЛЕЧЕНИЯ ШЛАНГОВ DN25
ДЛЯ ШТЫРЕВЫХ ШЛАНГОВ SAE

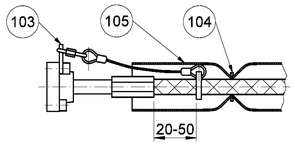

ASSEMBLY SCHEME FOR HOSE ANTIEXTRACTION SYSTEM DN32
FOR SAE FLANGE TYPE HOSE

СХЕМА СБОРКИ ДЛЯ СИСТЕМЫ ПРОТИВОИЗВЛЕЧЕНИЯ ШЛАНГОВ DN32
ДЛЯ ШТЫРЕВЫХ ШЛАНГОВ SAE

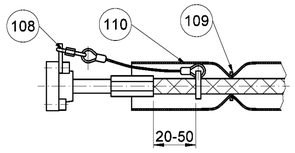

ПРИМЕЧАНИЕ:
- ПРИ МОНТАЖЕ СИСТЕМЫ ОПОРЫ, ПЛИТЫ И БЛОКИ ДОЛЖНЫ БЫТЬ ТОЧЕЧНОСВАРНЫМИ. ПОСЛЕ ЗАВЕРШЕНИЯ ВСЕЙ СИСТЕМЫ, НАНЕСТИ ПРОПЛАВНОЙ ШОВ
- СОЕДИНИТЕЛЬНЫЕ УСТРОЙСТВА ДОЛЖНЫ БЫТЬ УСТАНОВЛЕНЫ РЯДОМ С СОЕДИНЕНИЯМИ ОСНОВНЫХ ЭЛЕМЕНТОВ МАШИН ДЛЯ ПРЕДОСТАВЛЕНИЯ ВОЗМОЖНОСТИ ОТДЕЛЕНИЯ В БУДУЩЕМ
- ТРАЕКТОРИЯ ТРУБОПРОВОДОВ И РАЗМЕРЫ ПОЗИЦИОНИРОВАНИЯ ПОДЛЕЖАТ ПРОВЕРКЕ ПРИ СБОРКЕ ПО ОТНОШЕНИЮ К ВОЗМОЖНЫМ ЧАСТИЧНЫМ ПОМЕХАМИ С ЧАСТЯМИ МАШИНЫ И/ИЛИ ДРУГИМИ ЧАСТЯМИ, НЕ ВЫДЕЛЕННЫМИ НА СТАДИИ ПЛАНИРОВАНИЯ.
- ПОДДЕРЖАНИЕ ТРУБ ЗАЖИМАМИ И ПРОФИЛЯМИ, УКАЗАННЫЕ В ВЕДОМОСТИ МАТЕРИАЛОВ И ПРЕДСТАВЛЕННЫЕ НА ЧЕРТЕЖЕ, ЯВЛЯЮТСЯ ОРИЕНТИРОВОЧНЫМИ И МОГУТ БЫТЬ ИЗМЕНЕНЫ ПРИ МОНТАЖЕ
- ШЛАНГИ ДОЛЖНЫ ПРОХОДИТЬ СВОБОДНО БЕЗ СОЗДАНИЯ ПОМЕХ С ДРУГИМИ ЧАСТЯМИ И/ИЛИ НЕПОДВИЖНЫМИ ЧАСТЯМИ МАШИН
- СДЕЛАТЬ ОТВЕРСТИЯ В ПЕРЕХОДНЫХ МОСТИКАХ И/ИЛИ ОГРАЖДЕНИЯХ В СООТВЕТСТВИИ С ТРЕБУЕМОЙ ТРАЕКТОРИЕЙ ТРУБОПРОВОДОВ.

NOTES
- DURING THE SYSTEM ASSEMBLING SUPPORTS,PLATES AND BLOCK MUST BE SPOT WELDED.ASTER COMPLETE ALL SYSTEM PLEASE FULLWELD.
- CONNECTORS HAVE TO BE INSTALLED NEAR THE JUNCTIONS OF MAIN MACHINE ELEMENTS TO ENABLE FUTURE SEPARATION
- PIPE PATHS AND POSITIONING DIMENSIONS TO BE VERIFIED AT ASSEMBLY IN RELATIONSHIP WITH POSSIBLE PARTIAL INTERFERENCES WITH MACHINE PARTS AND/OR OTHER PLANTS NOT EVIDENCED IN THE PLANNING PHASE
- PIPE SUPPORT BY FASTENING CLAMPS AND PROFILES IN THE B.O.M. AND REPRESENTED ON DRAWING IS INDICATIVE AND CAN BE MODIFIED AT ASSEMBLY
- HOSES HAVE TO RUN FREELY WITHOUT ANY INTERFERENCE WITH OTHER PLANTS AND/OR MACHINE FIXED PARTS.
- MAKE OPENINGS ON WALKWAYS AND/OR ON GUARDS IN ACCORDANCE WITH PIPES PATH REQUEST

WELDS AS PER DANIELI STD 2.8.006
СВАРКА ПО СТАНДАРТУ ДАНИЕЛИ 2.8.006
WELDS TO BE DONE ON SITE
СВАРКУ ВЫПОЛНИТЬ ПРИ МОНТАЖЕ
WELDS TO BE DONE ON WORKSHOP
СВАРКУ ВЫПОЛНИТЬ В ЦЕХЕ
WHERE NOT INDICATED A = 0.7 OF
MINIMUM THICKNESS TO BE WELDED
ГДЕ НЕ УКАЗАНО A = 0.7 ОТ МИНИМАЛЬНОЙ
ТОЛЩИНЫ СВАРИВАЕМЫХ ДЕТАЛЕЙ
CLASS : A
КЛАСС :

Rev.	Date	Revisions description	Drawn by	Checked by	Approved by
00	31 Jan 2020	EMISSIONE ISSUED	Bhimered U	Pawar N	Del F

Material 1 (where not indicated on drawing) — State of supply Mat.1 Danieli Supply Std. — Supply Class — Pattern DB
Material 2 — State of supply Mat.2 Danieli Supply Std. — Supply Class — Casting code
Material 1 Equivalent
Heat Treatment
On Drawing Symbol, if required,
Coating
On Drawing Symbol, if required,
Unquoted radius (mm) — Unquoted bevels (mm) — Dimensions without tolerance as per DANIELI STD 2.4.103 — Machinings — Prec.Class A — Max.Welding Class B
Project Name

DANIELI CENTRO MET

Job nr
Obtained from 8.833921.K
Replaces
Family code/Machine code ICIPWI
Weight (Kg) 325 — d (Kgm³)

Title: HYDRAULIC SYSTEM
Scale 1:50
DANIELI Shop number 8.890431.V
Revision 00
Format A1
Nr. of sheets 001
DANIELI dwg number
Revision
Sheet 001 Follow

Copyright © Danieli & C. Officine Meccaniche S.p.A. 2019 – All rights reserved. CONFIDENTIAL. Property of Danieli & C. Officine Meccaniche S.p.A. Unauthorized reproduction, copying, distribution or any other use of the whole or any part of this documentation is strictly prohibited.

File nr FD12-012-131-426.IDW

COMPUTER AIDED DESIGN – 1

COP41295-1 DPC13Y023712 GS57 8.834046.S