




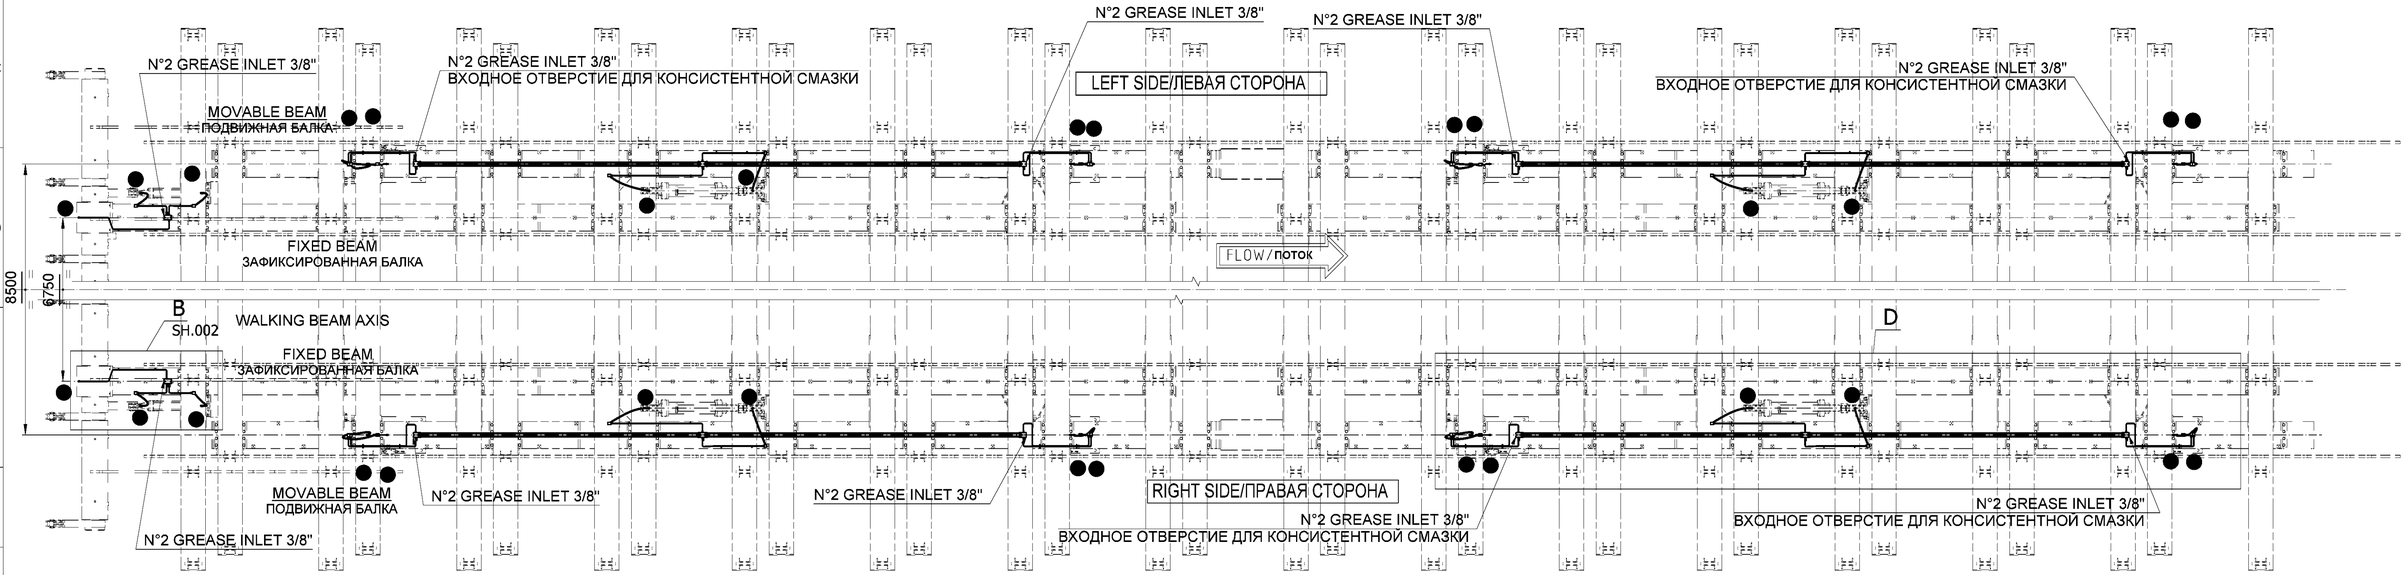


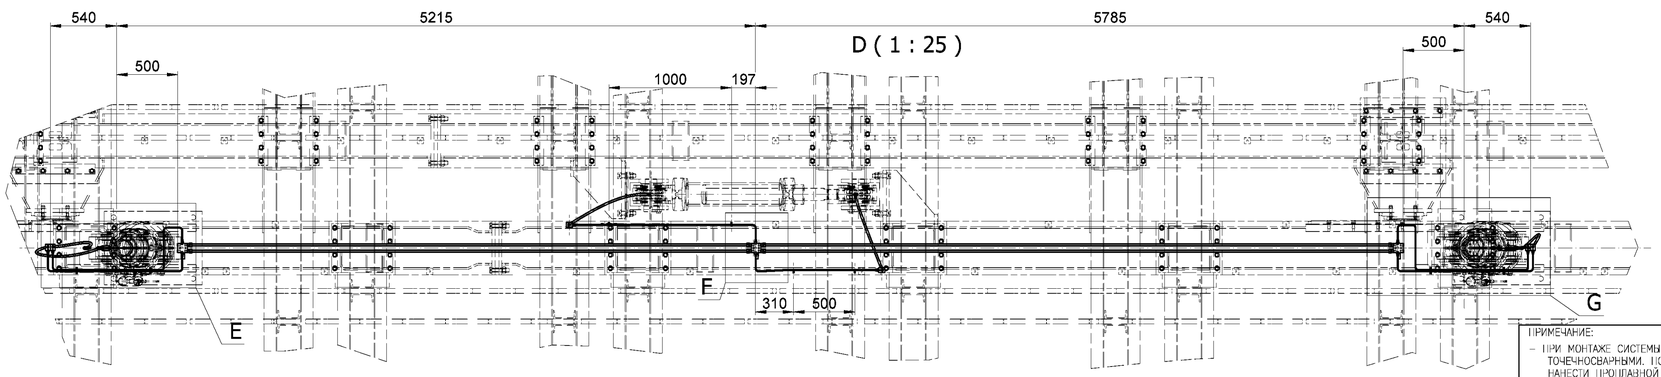

E (1 : 10)

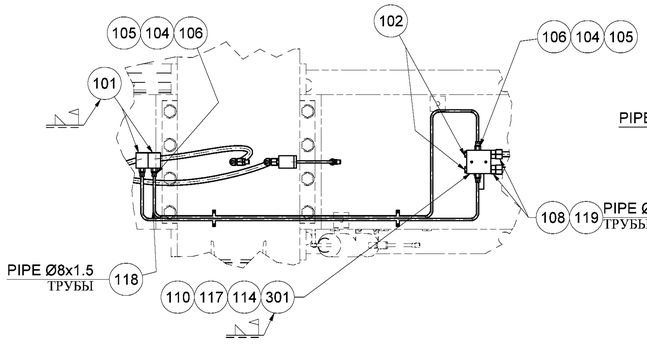

F (1 : 10)

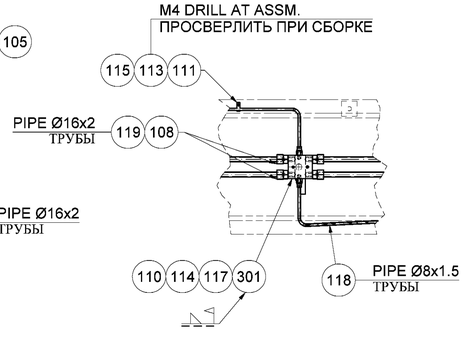

GREASE SYSTEM: LEGEND & POINTS Q.TY
СИСТЕМА КОНСИСТЕНТНОЙ СМАЗКИ:
ЭКСПЛИКАЦИЯ И КОЛИЧЕСТВО ТОЧЕК

N°30	АВТОМАТИЧЕСКИЕ ЦЕНТРАЛИЗОВАННЫЕ ТОЧКИ: AUTOMATIC CENTRALIZED POINTS ●
N°-	ЦЕНТРАЛИЗОВАННЫЕ РУЧНЫЕ ТОЧКИ: CENTRALIZED MANUAL POINTS ▼
N°-	МЕЧТНЫЕ РУЧНЫЕ ТОЧКИ: LOCAL MANUAL POINTS ■

WELDS AS PER DANIELI STD 2.8.006
СВАРКА ПО СТАНДАРТУ ДАНИЕЛИ 2.8.006

WELDS TO BE DONE ON SITE
СВАРКУ ВЫПОЛНИТЬ ПРИ МОНТАЖЕ

WELDS TO BE DONE ON WORKSHOP
СВАРКУ ВЫПОЛНИТЬ В ЦЕХЕ

WHERE NOT INDICATED A = 0.7 OF MINIMUM THICKNESS TO BE WELDED
ГДЕ НЕ УКАЗАНО A = 0.7 ОТ МИНИМАЛЬНОЙ ТОЛЩИНЫ СВАРИВАЕМЫХ ДЕТАЛЕЙ

CLASS : A
КЛАСС :

ПРИМЕЧАНИЕ:
- ПРИ МОНТАЖЕ СИСТЕМЫ ОПОРЫ, ПЛИТЫ И БЛОКИ ДОЛЖНЫ БЫТЬ ТОЧЕЧНОСВАРНЫМИ. ПОСЛЕ ЗАВЕРШЕНИЯ ВСЕЙ СИСТЕМЫ, НАНЕСТИ ПРОПЛАВНОЙ ШОВ
- СОЕДИНИТЕЛЬНЫЕ УСТРОЙСТВА ДОЛЖНЫ БЫТЬ УСТАНОВЛЕНЫ РЯДОМ С СОЕДИНЕНИЯМИ ОСНОВНЫХ ЭЛЕМЕНТОВ МАШИН ДЛЯ ПРЕДОСТАВЛЕНИЯ ВОЗМОЖНОСТИ ОТДЕЛЕНИЯ В БУДУЩЕМ
- ТРАЕКТОРИЯ ТРУБОПРОВОДОВ И РАЗМЕРЫ ПОЗИЦИОНИРОВАНИЯ ПОДЛЕЖАТ ПРОВЕРКЕ ПРИ СБОРКЕ ПО ОТНОШЕНИЮ К ВОЗМОЖНЫМ ЧАСТИЧНЫМ ПОМЕХАМИ С ЧАСТЯМИ МАШИНЫ И/ИЛИ ДРУГИМИ ЧАСТЯМИ, НЕ ВЫДЕЛЕННЫМИ НА СТАДИИ ПЛАНИРОВАНИЯ.
- ПОДДЕРЖАНИЕ ТРУБ ЗАЖИМАМИ И ПРОФИЛЯМИ, УКАЗАННЫЕ В ВЕДОМОСТИ МАТЕРИАЛОВ И ПРЕДСТАВЛЕННЫЕ НА ЧЕРТЕЖЕ, ЯВЛЯЮТСЯ ОРИЕНТИРОВОЧНЫМИ И МОГУТ БЫТЬ ИЗМЕНЕНЫ ПРИ МОНТАЖЕ
- ШЛАНГИ ДОЛЖНЫ ПРОХОДИТЬ СВОБОДНО БЕЗ СОЗДАНИЯ ПОМЕХ С ДРУГИМИ ЧАСТЯМИ И/ИЛИ НЕПОДВИЖНЫМИ ЧАСТЯМИ МАШИН
- СДЕЛАТЬ ОТВЕРСТИЯ В ПЕРЕХОДНЫХ МОСТИКАХ И/ИЛИ ОГРАЖДЕНИЯХ В СООТВЕТСТВИИ С ТРЕБУЕМОЙ ТРАЕКТОРИЕЙ ТРУБОПРОВОДОВ.

NOTES
- DURING THE SYSTEM ASSEMBLING SUPPORTS,PLATES AND BLOCK MUST BE SPOT WELDED.ASTER COMPLETE ALL SYSTEM PLEASE FULLWELD.
- CONNECTORS HAVE TO BE INSTALLED NEAR THE JUNCTIONS OF MAIN MACHINE ELEMENTS TO ENABLE FUTURE SEPARATION
- PIPE PATHS AND POSITIONING DIMENSIONS TO BE VERIFIED AT ASSEMBLY IN RELATIONSHIP WITH POSSIBLE PARTIAL INTERFERENCES WITH MACHINE PARTS AND/OR OTHER PLANTS NOT EVIDENCED IN THE PLANNING PHASE
- PIPE SUPPORT BY FASTENING CLAMPS AND PROFILES IN THE B.O.M. AND REPRESENTED ON DRAWING IS INDICATIVE AND CAN BE MODIFIED AT ASSEMBLY
- HOSES HAVE TO RUN FREELY WITHOUT ANY INTERFERENCE WITH OTHER PLANTS AND/OR MACHINE FIXED PARTS.
- MAKE OPENINGS ON WALKWAYS AND/OR ON GUARDS IN ACCORDANCE WITH PIPES PATH REQUEST

Rev.	Date	Revisions description	Drawn by	Checked by	Approved by
00	05 Feb 2020	EMISSIONE ISSUED	Brimered U	Power N	Del F

Material 1 (where not indicated on drawing) — State of supply Mat.1 — Danieli Supply Std. — Supply Class — Pattern 09
Material 2 — State of supply Mat.2 — Danieli Supply Std. — Supply Class — Casting code
Material 1 Equivalent
Heat Treatment
On Drowing Symbol, if required,
Coating
On Drowing Symbol, if required,
Unquoted radius (mm) | Unquoted bevels (mm) | Dimensions without tolerance as per DANIELI STD 2.4.103 | Machinings | Prec.Class A | Max.Welding Class A

Project Name

DANIELI CENTRO MET

Job nr
Obtained from 8.833922.L
Replaces
Family code/Machine code ICGpwi
Weight (Kg) 170 | d (Kgm⁻³)

Title: GREASE SYSTEM

Scale 1:50
DANIELI Shop number 8.890432.W | Revision 00
Format A1
DANIELI dwg number | Revision
Nr. of sheets 002
Sheet 001 | Follow

Copyright © Danieli & C. Officine Meccaniche S.p.A. 2019 – All rights reserved. CONFIDENTIAL. Property of Danieli & C. Officine Meccaniche S.p.A. Unauthorized reproduction, copying, distribution or any other use of the whole or any part of this documentation is strictly prohibited.

File nr FD12-012-134-409.IDW

COMPUTER AIDED DESIGN – 1

8.834046.S H558 DPC13Y03712 COP41295-1