




BEAMS & LONG. MEMBERS PLAN VIEW
БАЛКИ И ПРОДОЛЬНЫЕ БАЛКИ ВИД СВЕРХУ

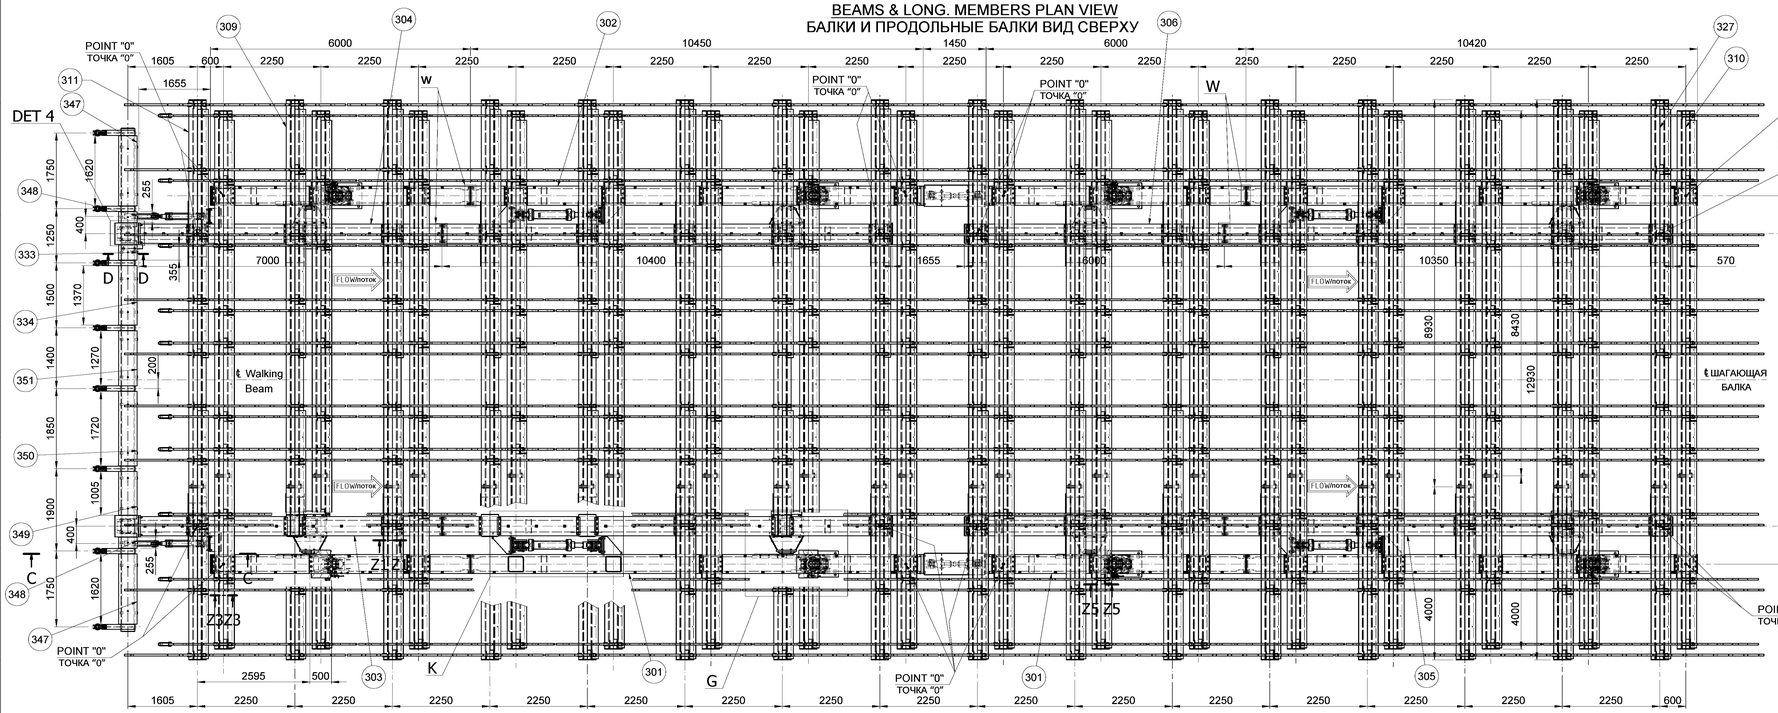


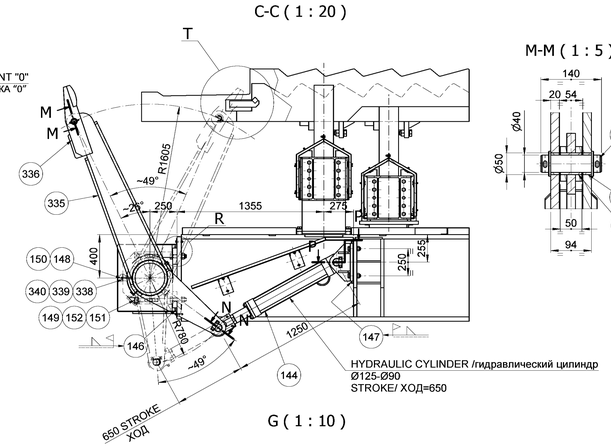


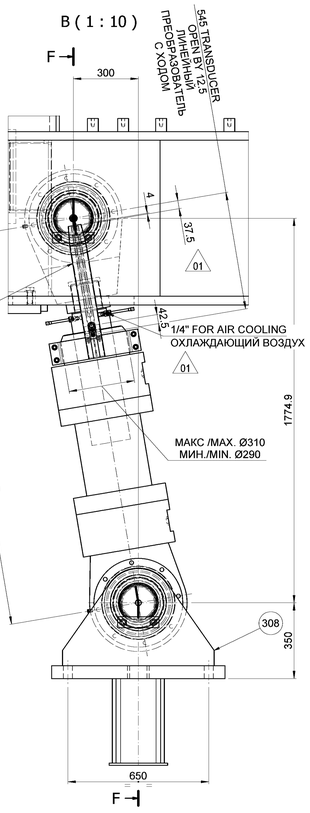


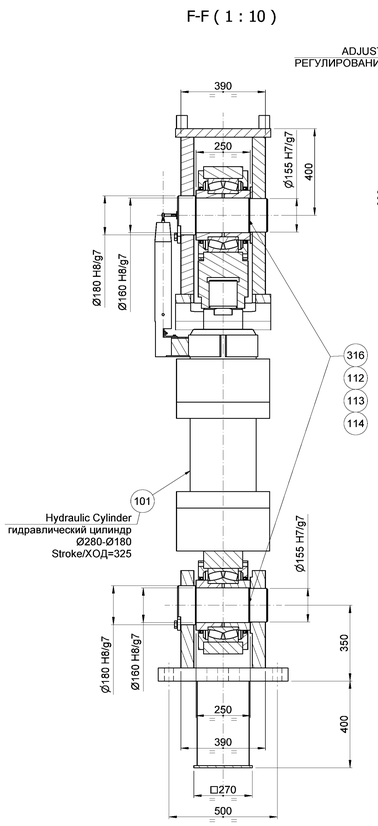

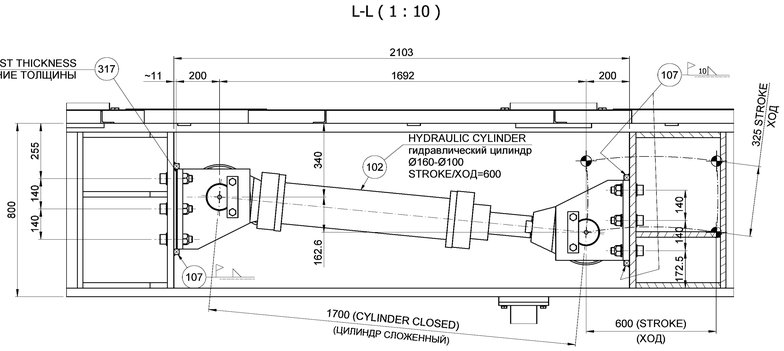

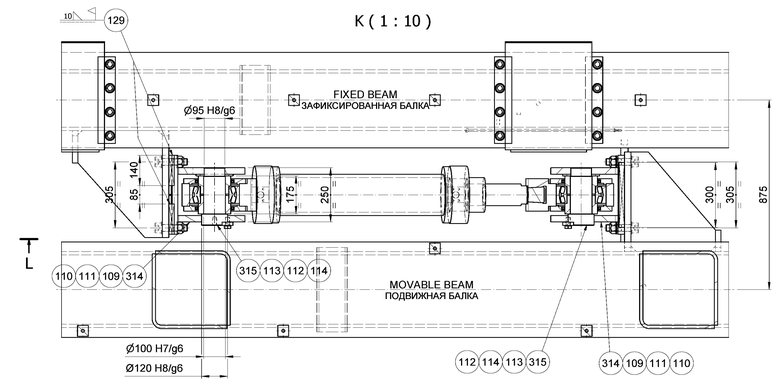

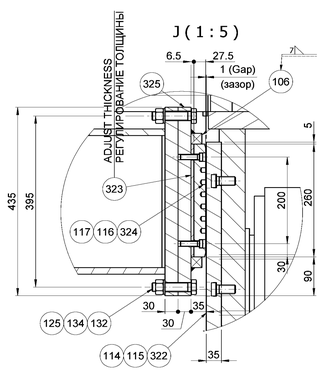

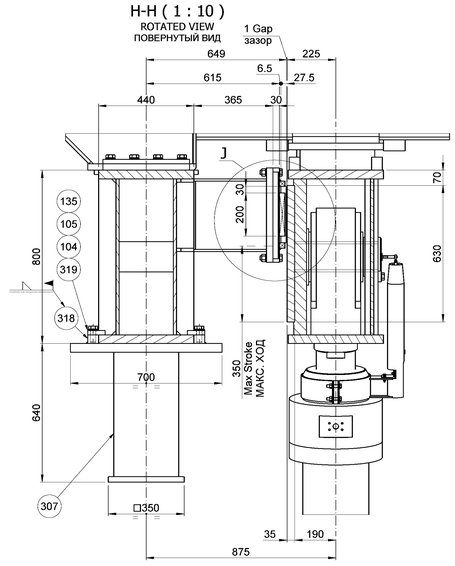

Rev.	Date	Revisions description	Drawn by	Checked by	Approved by
01	23 May 2020	MODIFICATO DOVE INDICATO REVISED WHERE INDICATED	Bhimsreed U	Powar N	Del F
00	21 Jan 2020	EMISSIONE ISSUED	Bhimsreed U	Powar N	Del F

Material 1 (where not indicated on drawing): State of supply Mat.1: Daniell Supply Std. Supply Class: Pattern SB

Material 2: State of supply Mat.2: Daniell Supply Std. Supply Class: Casting code

Material 1 Equivalent:

Heat Treatment:

On Drawing Symbol, if required:

Cooling:

On Drawing Symbol, if required:

Unspecified radius (mm) | Unspecified Bevels (mm) | Dimensions without tolerance as per: DANIELI STD 2.4.103 | Machinings | Prev.Class: B | Max Welding Class: A

Project Name:

DANIELI CENTRO MET

Job nr: 8.391299.P
Obtained from:
Replaces:

Family code/Machine code: PWI386 129 36 L 650
Weight (Kg): 280275
J (Kgm²):

Title: WALKING BEAM

Scale: 1:50

DANIELI Drop number: 8.834046.S

Revision: 01

Format: A0

Nr. of sheets: 003

DANIELI dwg number:

Revision:

Group: 002

Follow:

2020

File nr: FD12-008-381-593.IDW

COMPUTER AIDED DESIGN - 1

DPC13Y023712 B010 DPC13Y023712 COP41295-1