


ПОДВИЖНАЯ РЕЙКА/ MOVABLE RAKE 36111 ((N°96 PASSI/STEPS x350)+365+363+360+358+355+355+355)
НЕПОДВИЖНАЯ РЕЙКА/ FIXED RAKE 36111((N°96 PASSI/STEPS x350)+365+363+360+358+355+355+355)

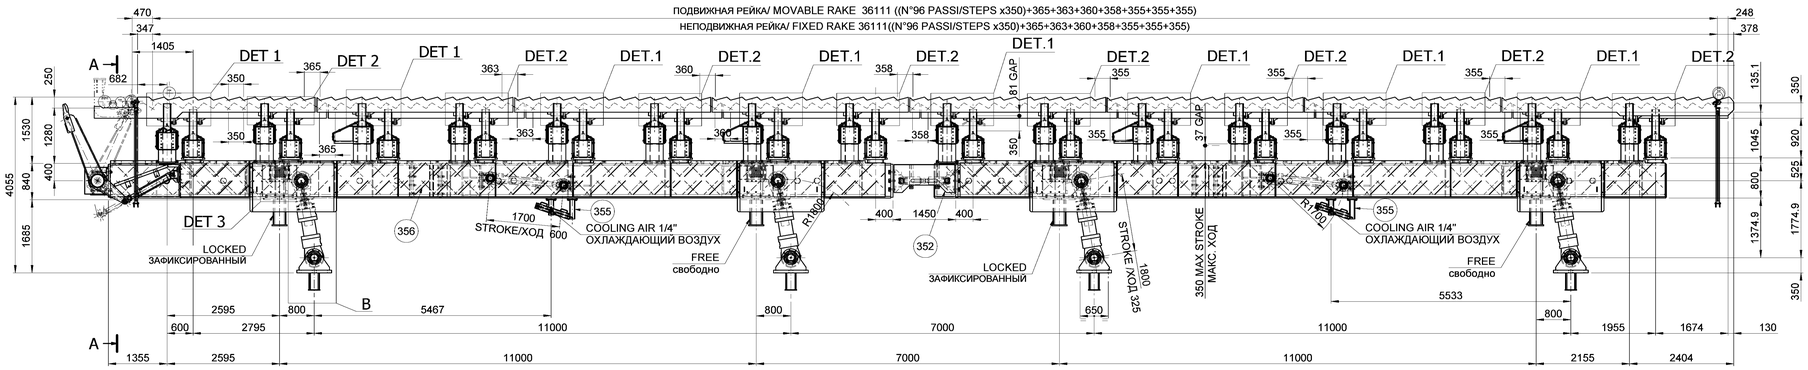


M1-M1 (1 : 10)

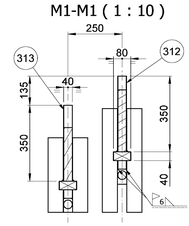


DET 1 (1 : 10)

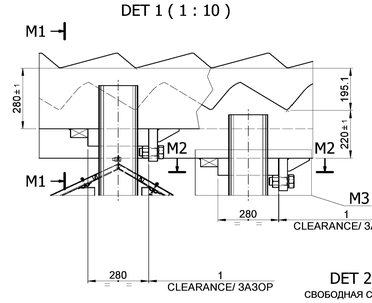


DET 2 (1 : 10)
СВОБОДНАЯ СТОРОНА/FREE SIDE

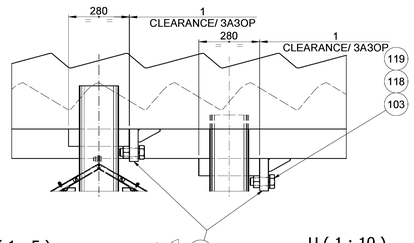


37836 (FIXED RAKE/ НЕПОДВИЖНАЯ РЕЙКА)

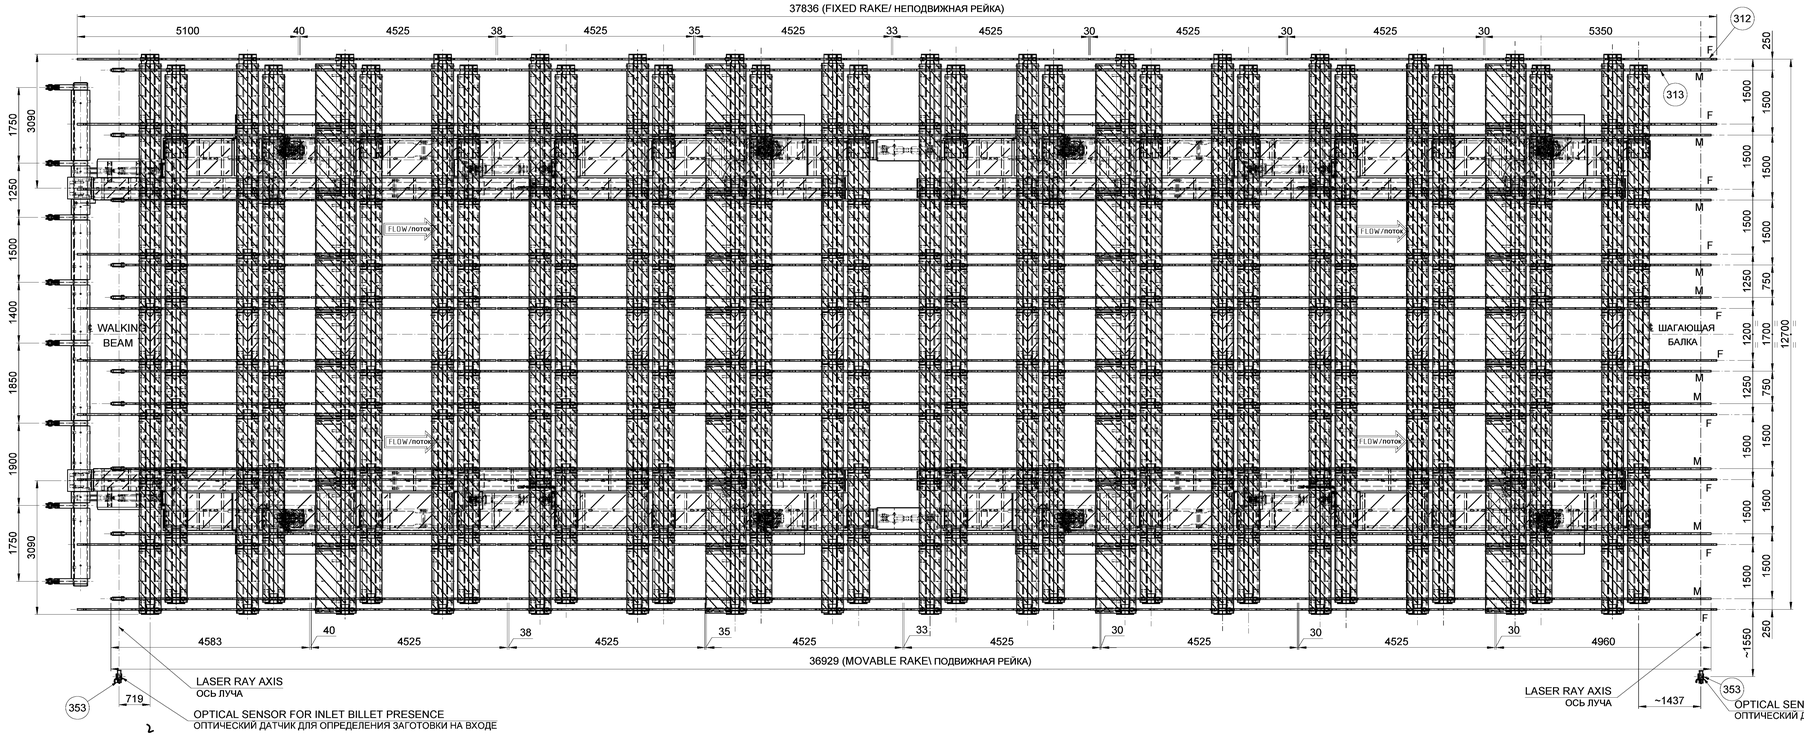

M3 (1 : 5)

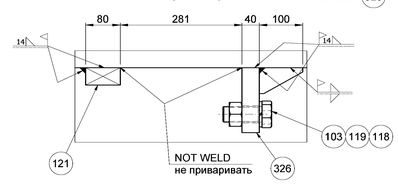

U (1 : 10)

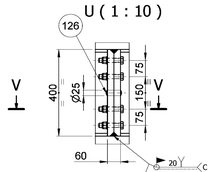

M2-M2 (1 : 10)

V-V (1 : 10)

DET 3 (1 : 10)

NOTE: BOLT TIGHTENING AS PER DANIELI STD 2.4.603
ЗАТЯЖКА БОЛТОВ ДОЛЖНА ОСУЩЕСТВЛЯТЬСЯ СОГЛАСНО СТАНДАРТУ DANIELI 2.4.603

(*)= С ЗАЗОРОМ 1 мм МЕЖДУ СКОЛЬЗЯЩЕЙ ПЛАСТИНОЙ И ПЛИТОЙ
WITH 1mm GAP BETWEEN SLIDING SHOE-PLATE

WELDS AS PER DANIELI STD 2.8.006
СВАРКА ПО СТАНДАРТУ ДАНИЕЛИ 2.8.006


WELDS TO BE DONE ON SITE
СВАРКУ ВЫПОЛНИТЬ ПРИ МОНТАЖЕ

WELDS TO BE DONE ON WORKSHOP
СВАРКУ ВЫПОЛНИТЬ В ЦЕХЕ

WHERE NOT INDICATED A = 0,7 OF MINIMUM THICKNESS TO BE WELDED
ГДЕ НЕ УКАЗАНО A = 0,7 ОТ МИНИМАЛЬНОЙ ТОЛЩИНЫ СВАРИВАЕМЫХ ДЕТАЛЕЙ

CLASS : A
КЛАСС :

A-A (1 : 50)

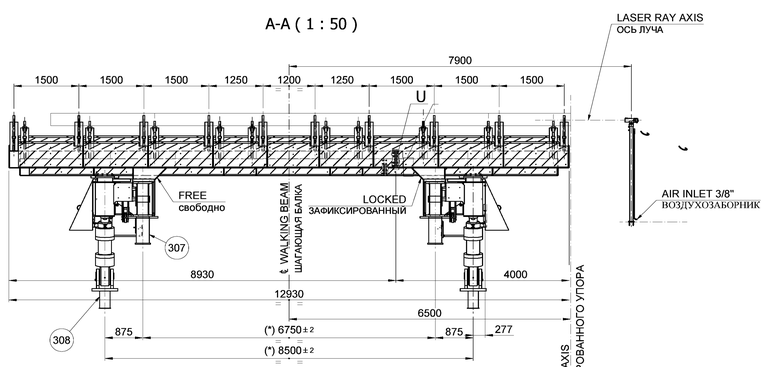

362 CYLINDER DISMOUNTING DIAGRAM
СХЕМА ДЕМОНТАЖА ЦИЛИНДРА

361 BLOOMS MOTION DIAGRAM
ДИАГРАММА ДВИЖЕНИЯ ЗАГОТОВОК


360 LONG. MEMBERS & RAKES MARKS POSITION
ПРОДОЛЬНЫЕ БАЛКИ И РАСПОЛОЖЕНИЕ РЕЕК

359 DEVICE LOCATION
РАЗМЕЩЕНИЕ ПРИБОРОВ

358 GREASE SYSTEM
система смазки

357 HYDRAULIC SYSTEM
ГИДРАВЛИЧЕСКАЯ СИСТЕМА

ISOMETRIC VIEW
ИЗОМЕТРИЧЕСКОЕ ИЗОБРАЖЕНИЕ

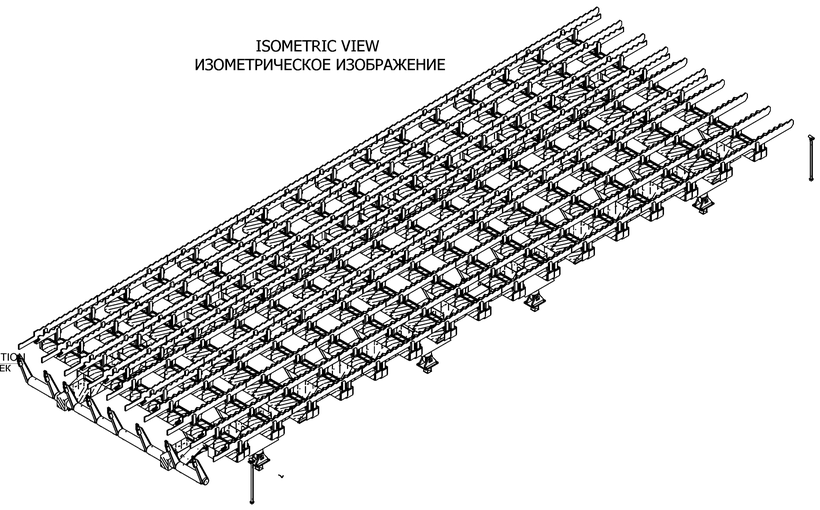

Rev.	Date	Revisions description	Drawn by	Checked by	Approved by
01	23 May 2020	MODIFICATO DOVE INDICATO REVISED WHERE INDICATED	Bhimsen U	Power N	Del F
00	21 Jan 2020	EMISSIONE ISSUED	Bhimsen U	Power N	Del F

Material 1 (where not indicated on drawing) — State of supply Mat.1 — Danieli Supply Std. — Supply Class — Pattern 08
Material 2 — State of supply Mat.2 — Danieli Supply Std. — Supply Class — Casting code
Material 1 Equivalent
Heat Treatment
On Drawing Symbol, if required,
Coating
On Drawing Symbol, if required,
Unquoted radius (mm) — Unquoted Bevels (mm) — Dimensions without tolerance as per DANIELI STD 2.4.103 — Machinings — Prec.Class B — Max Welding Class A

Project Name

DANIELI CENTRO MET

Job nr
Obtained from 8.391299.P
Replaces

Family code/Machine code PWLS86 129 36 L 650
Weight (Kg) 280275 J (Kgm²)

Title: WALKING BEAM

DANIELI Shop number 8.834046.S
DANIELI dwg number
Revision 01
Revision
Scale 1:50
Format A0
No. of sheets 003
Sheet 001 Follow

2020

File nr FD12-008-379-859.IDW

DPC13Y02372 8010 DPC13Y02372 COP41295.1

COMPUTER AIDED DESIGN - I